


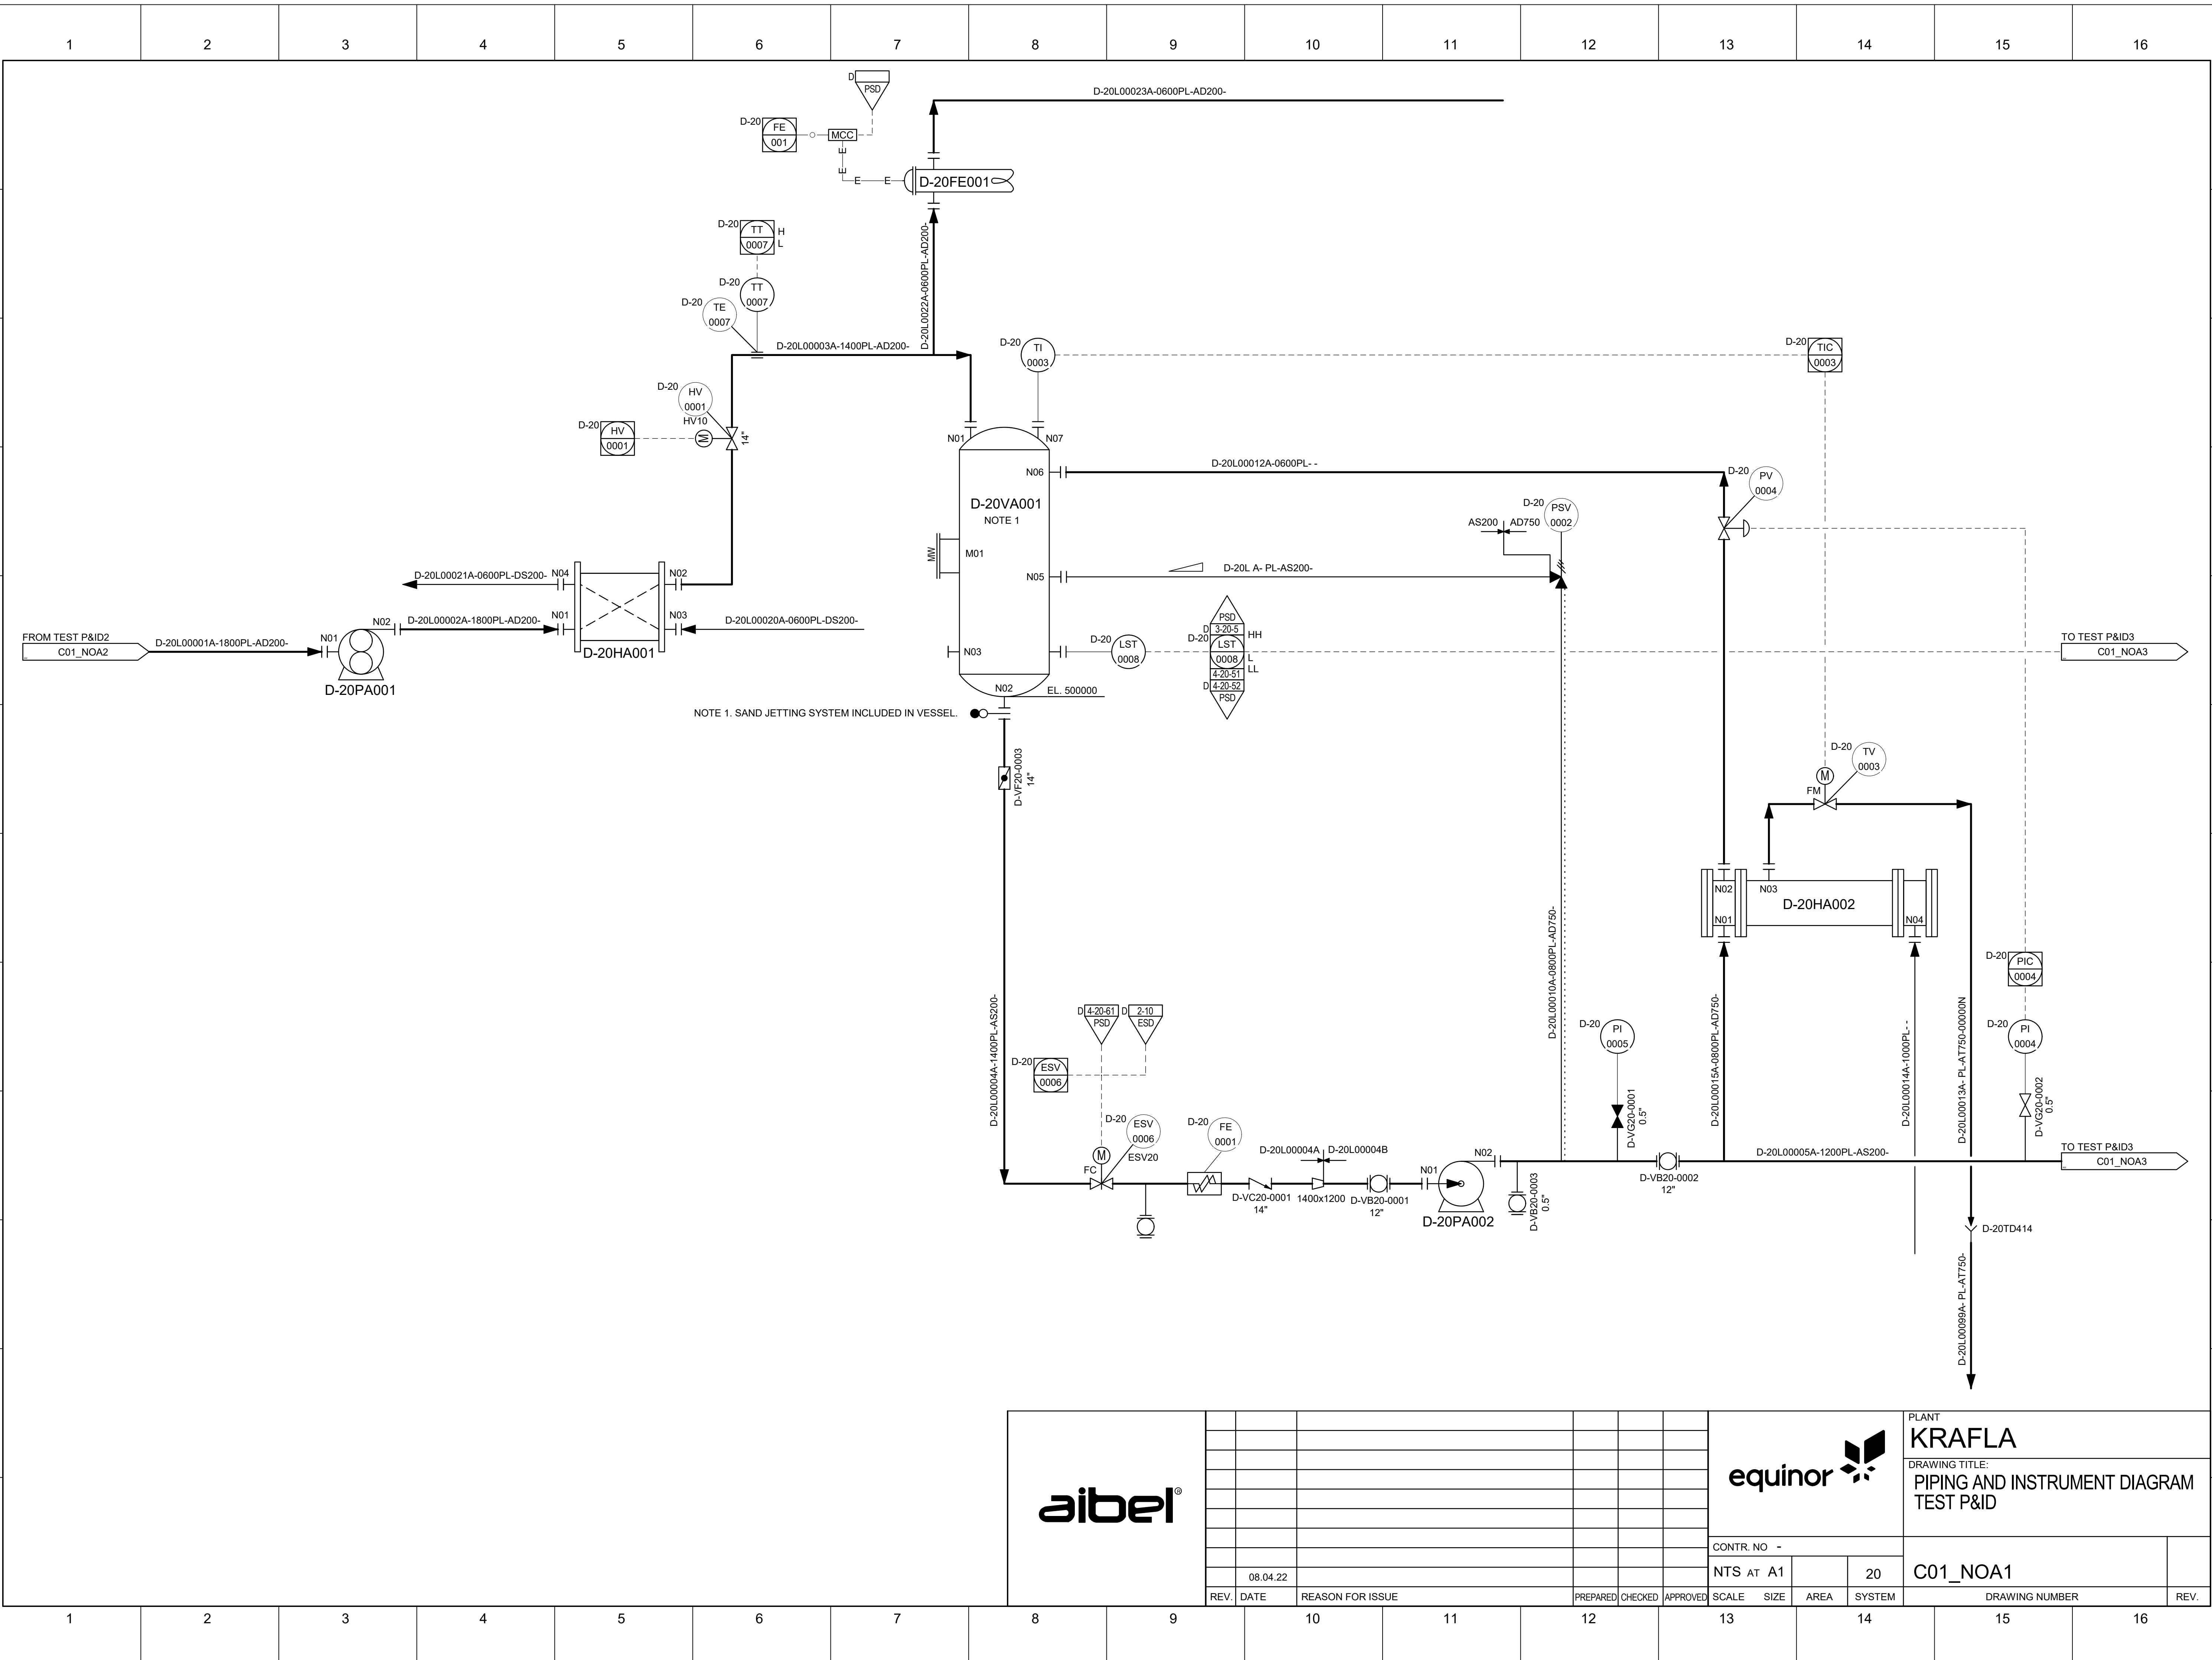

|                                                                                       |          |                  |  |  |  |          |                                                                                       |             |       |      |                |          |                                            |  |  |  |      |
|---------------------------------------------------------------------------------------|----------|------------------|--|--|--|----------|---------------------------------------------------------------------------------------|-------------|-------|------|----------------|----------|--------------------------------------------|--|--|--|------|
|  |          |                  |  |  |  |          |  |             |       |      | PLANT          |          | KRAFLA                                     |  |  |  |      |
|                                                                                       |          |                  |  |  |  |          |                                                                                       |             |       |      | DRAWING TITLE: |          | PIPING AND INSTRUMENT DIAGRAM<br>TEST P&ID |  |  |  |      |
|                                                                                       |          |                  |  |  |  |          |                                                                                       |             |       |      |                |          |                                            |  |  |  |      |
|                                                                                       |          |                  |  |  |  |          |                                                                                       | CONTR. NO - |       |      |                |          |                                            |  |  |  |      |
|                                                                                       | 08.04.22 |                  |  |  |  |          | NTS AT A1                                                                             |             |       |      | 20             | C01_NOA1 |                                            |  |  |  |      |
| REV.                                                                                  | DATE     | REASON FOR ISSUE |  |  |  | PREPARED | CHECKED                                                                               | APPROVED    | SCALE | SIZE | AREA           | SYSTEM   | DRAWING NUMBER                             |  |  |  | REV. |