


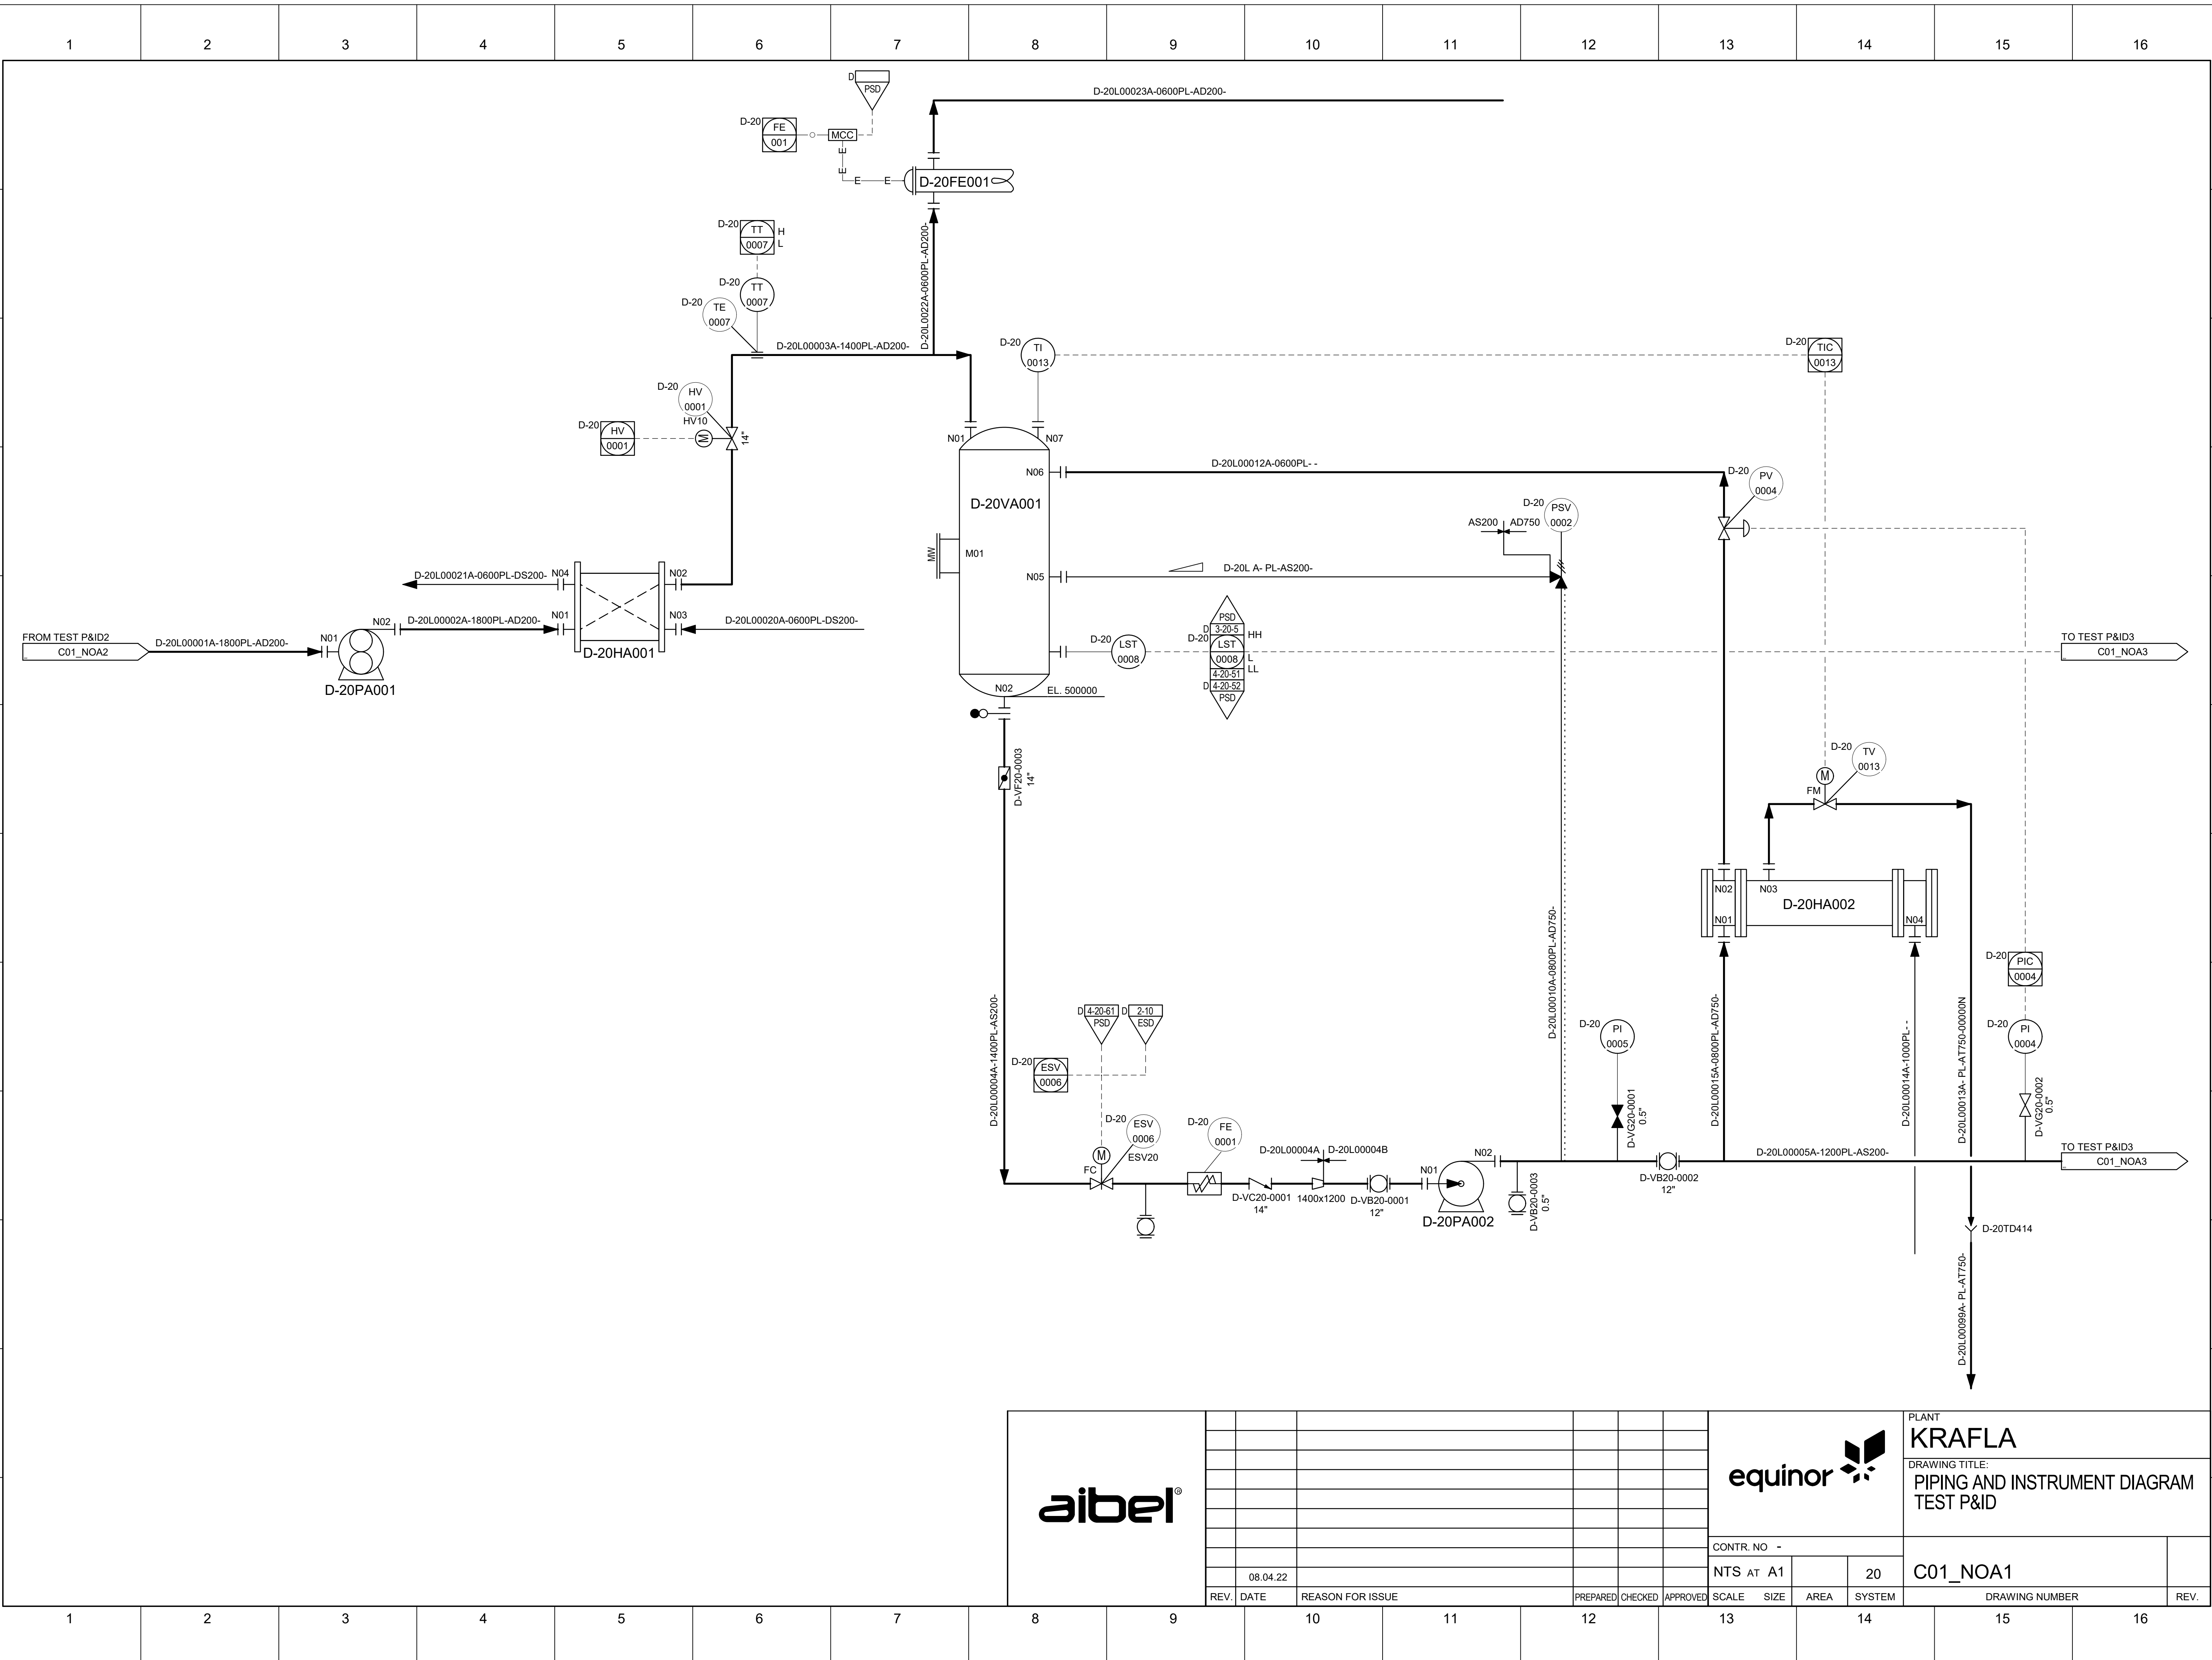

											PLANT KRAFLA				
											DRAWING TITLE: PIPING AND INSTRUMENT DIAGRAM TEST P&ID				
							CONTR. NO -								
							NTS AT A1			20	C01_NOA1				
		08.04.22													
REV.	DATE	REASON FOR ISSUE				PREPARED	CHECKED	APPROVED	SCALE	SIZE	AREA	SYSTEM	DRAWING NUMBER		REV.