


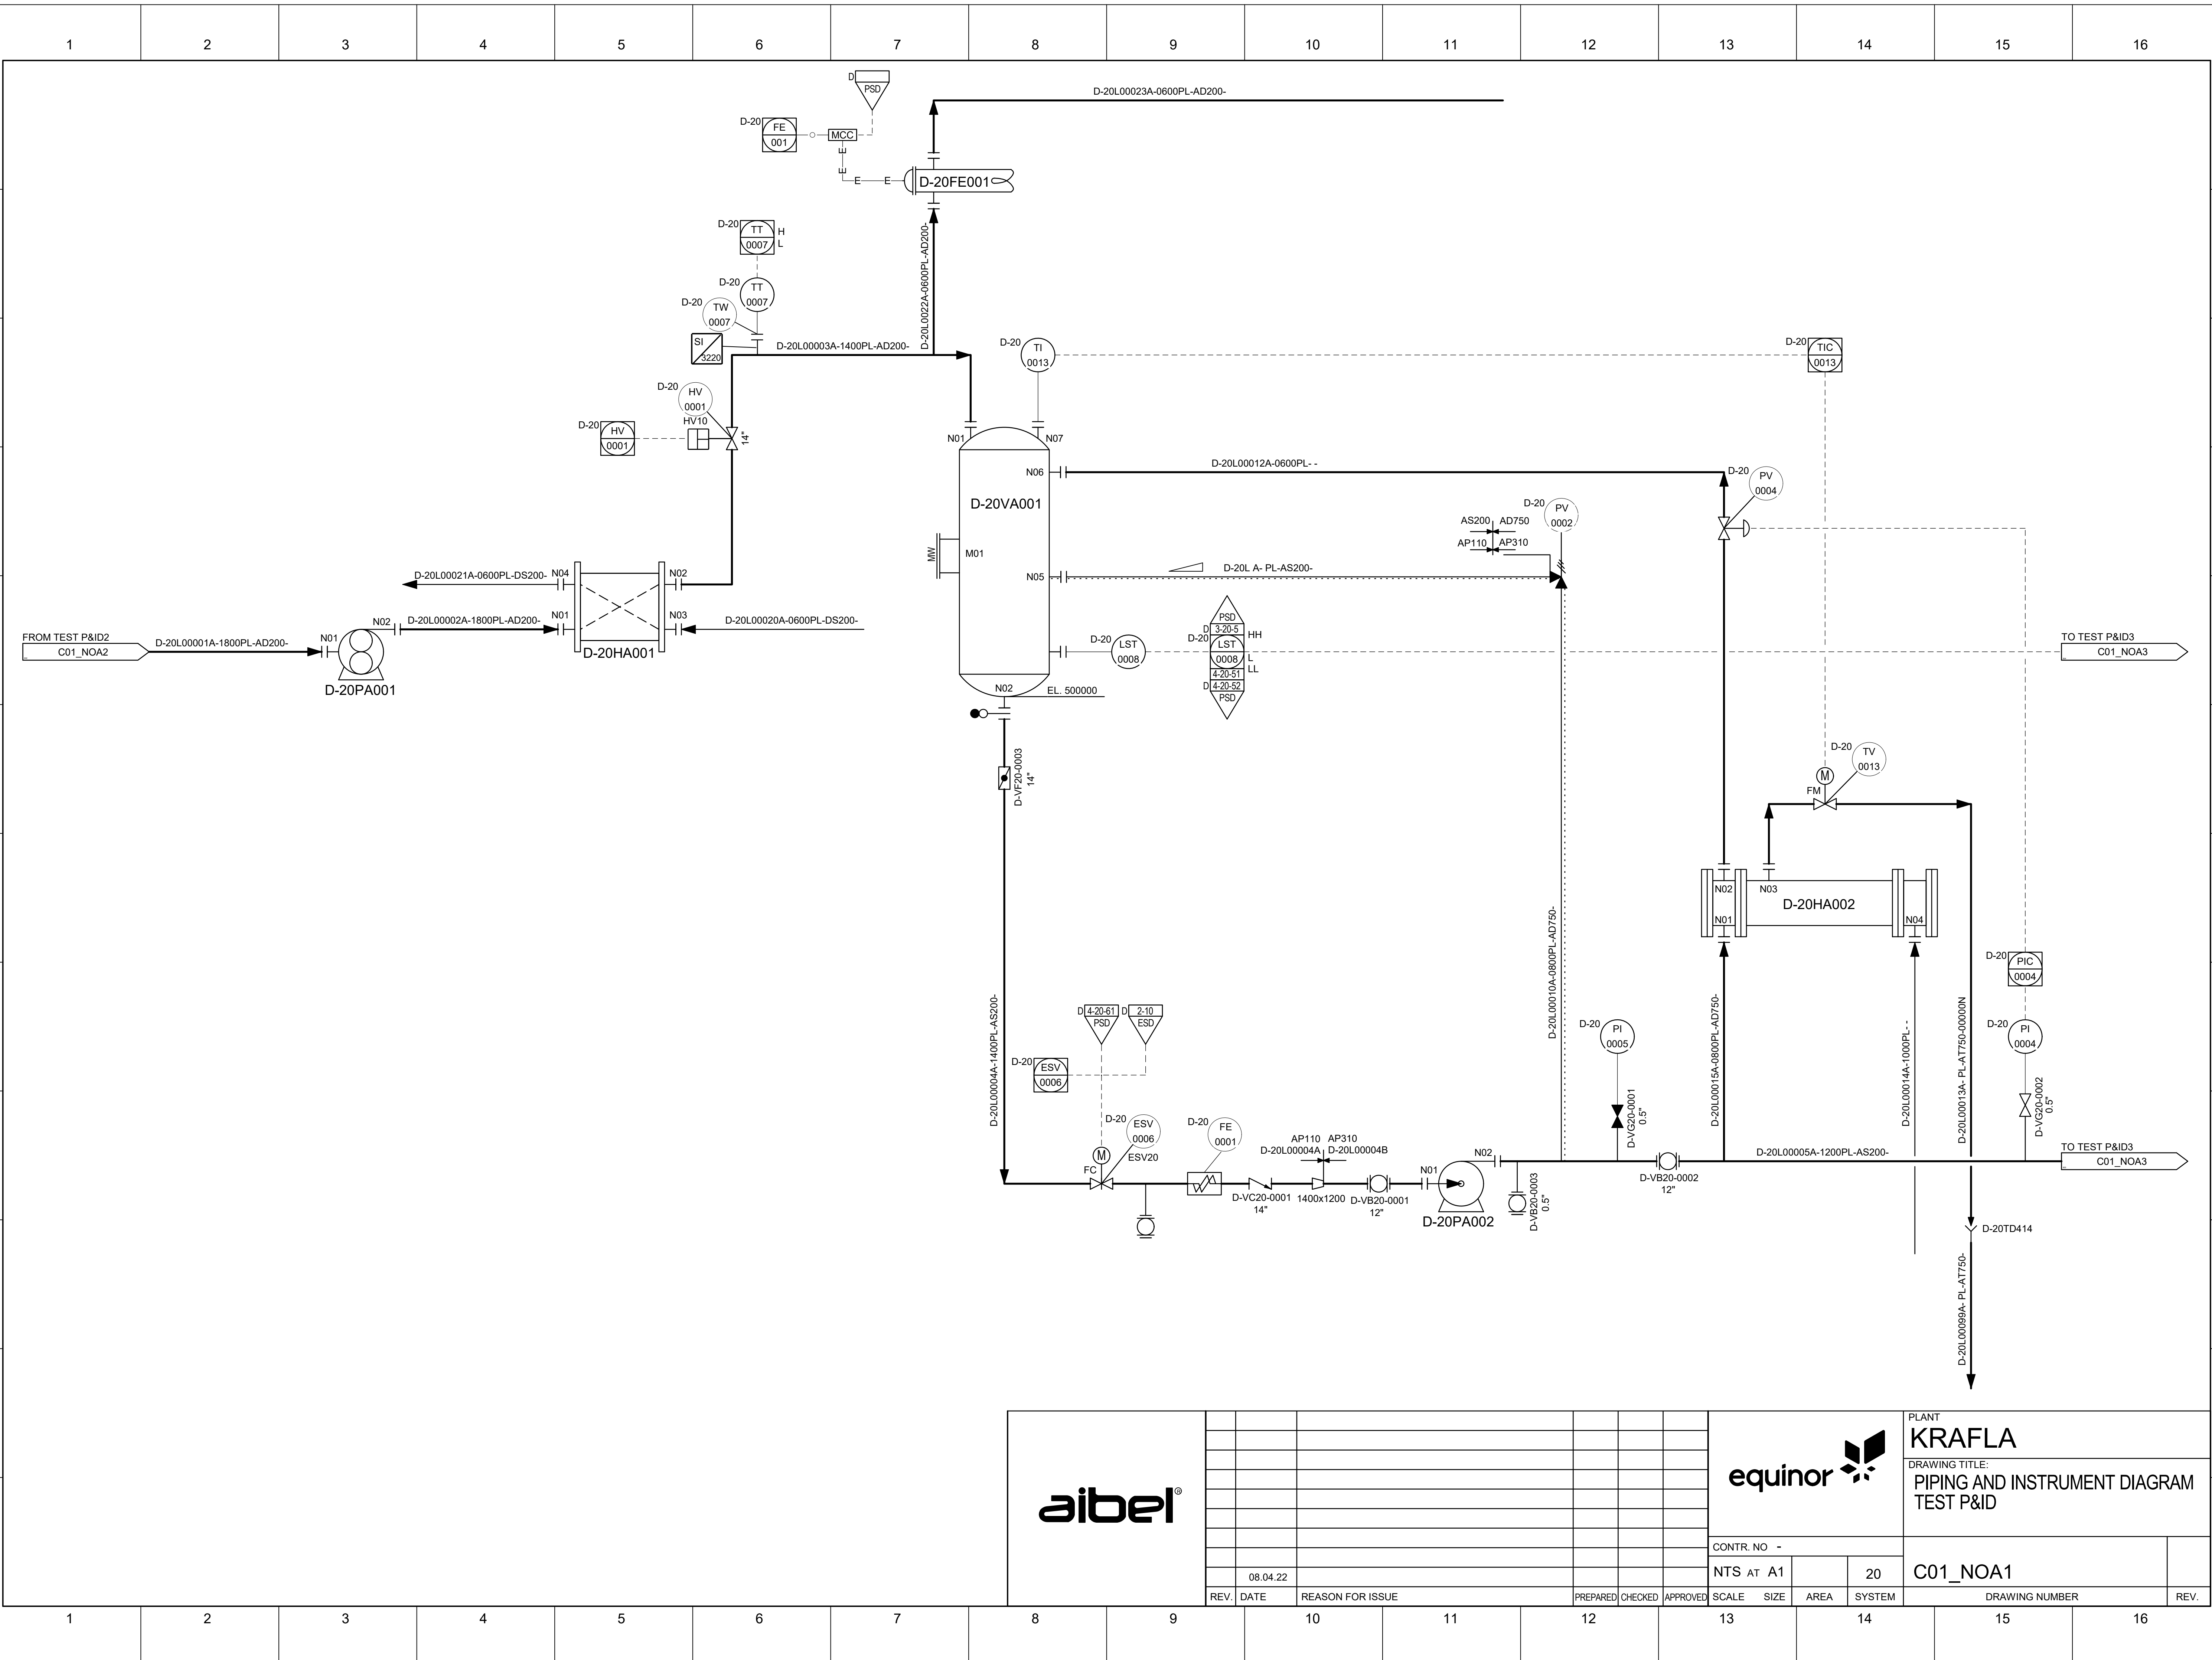

PLANT		KRAFLA	
DRAWING TITLE:		PIPING AND INSTRUMENT DIAGRAM TEST P&ID	
CONTR. NO -			
NTS AT A1		20	
C01_NOA1			
DRAWING NUMBER			
REV.			

REV.	DATE	REASON FOR ISSUE	PREPARED	CHECKED	APPROVED	SCALE	SIZE	AREA	SYSTEM
	08.04.22								