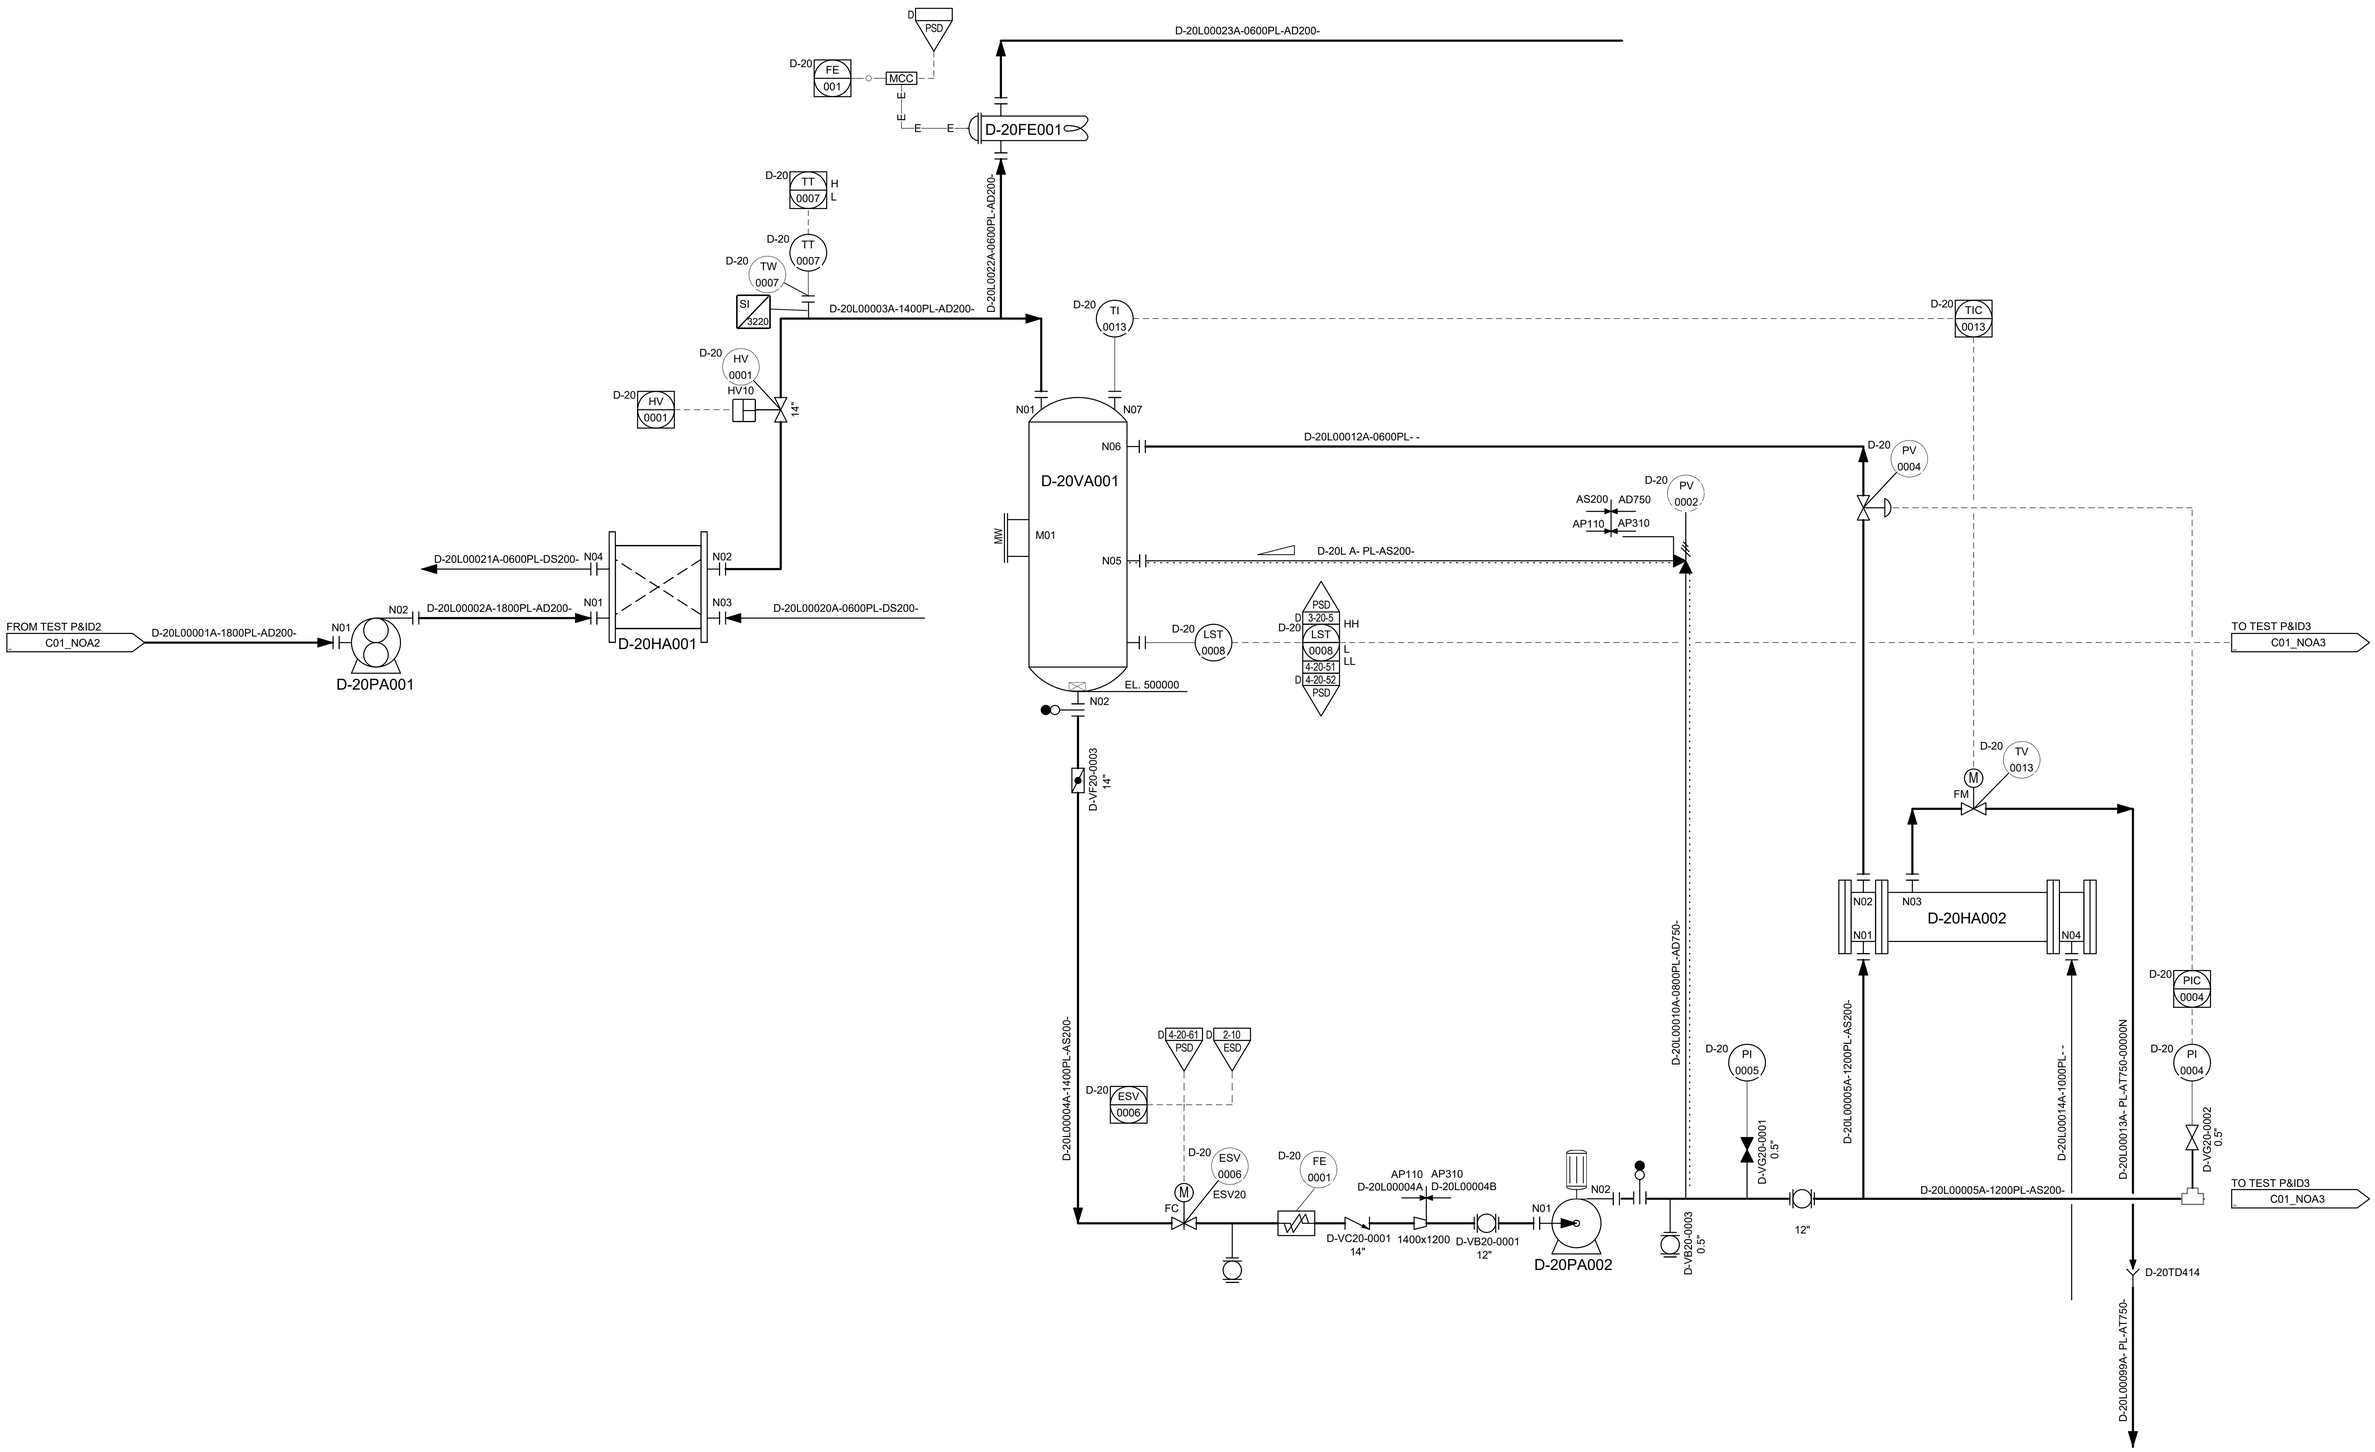


| REV. | DATE | REASON FOR ISSUE | PREPARED | CHECKED | APPROVED |
|---|---|---|---|---|---|
| | 08.04.22 | | | | |

aibel

equinor

PLANT: KRAFLA

DRAWING TITLE: PIPING AND INSTRUMENT DIAGRAM TEST P&ID

CONTR. NO -

| SCALE | SIZE | AREA | SYSTEM | DRAWING NUMBER | REV. |
|---|---|---|---|---|---|
| NTS AT | A1 | | 20 | C01_NOA1 | |

BORDER_CP_A1