


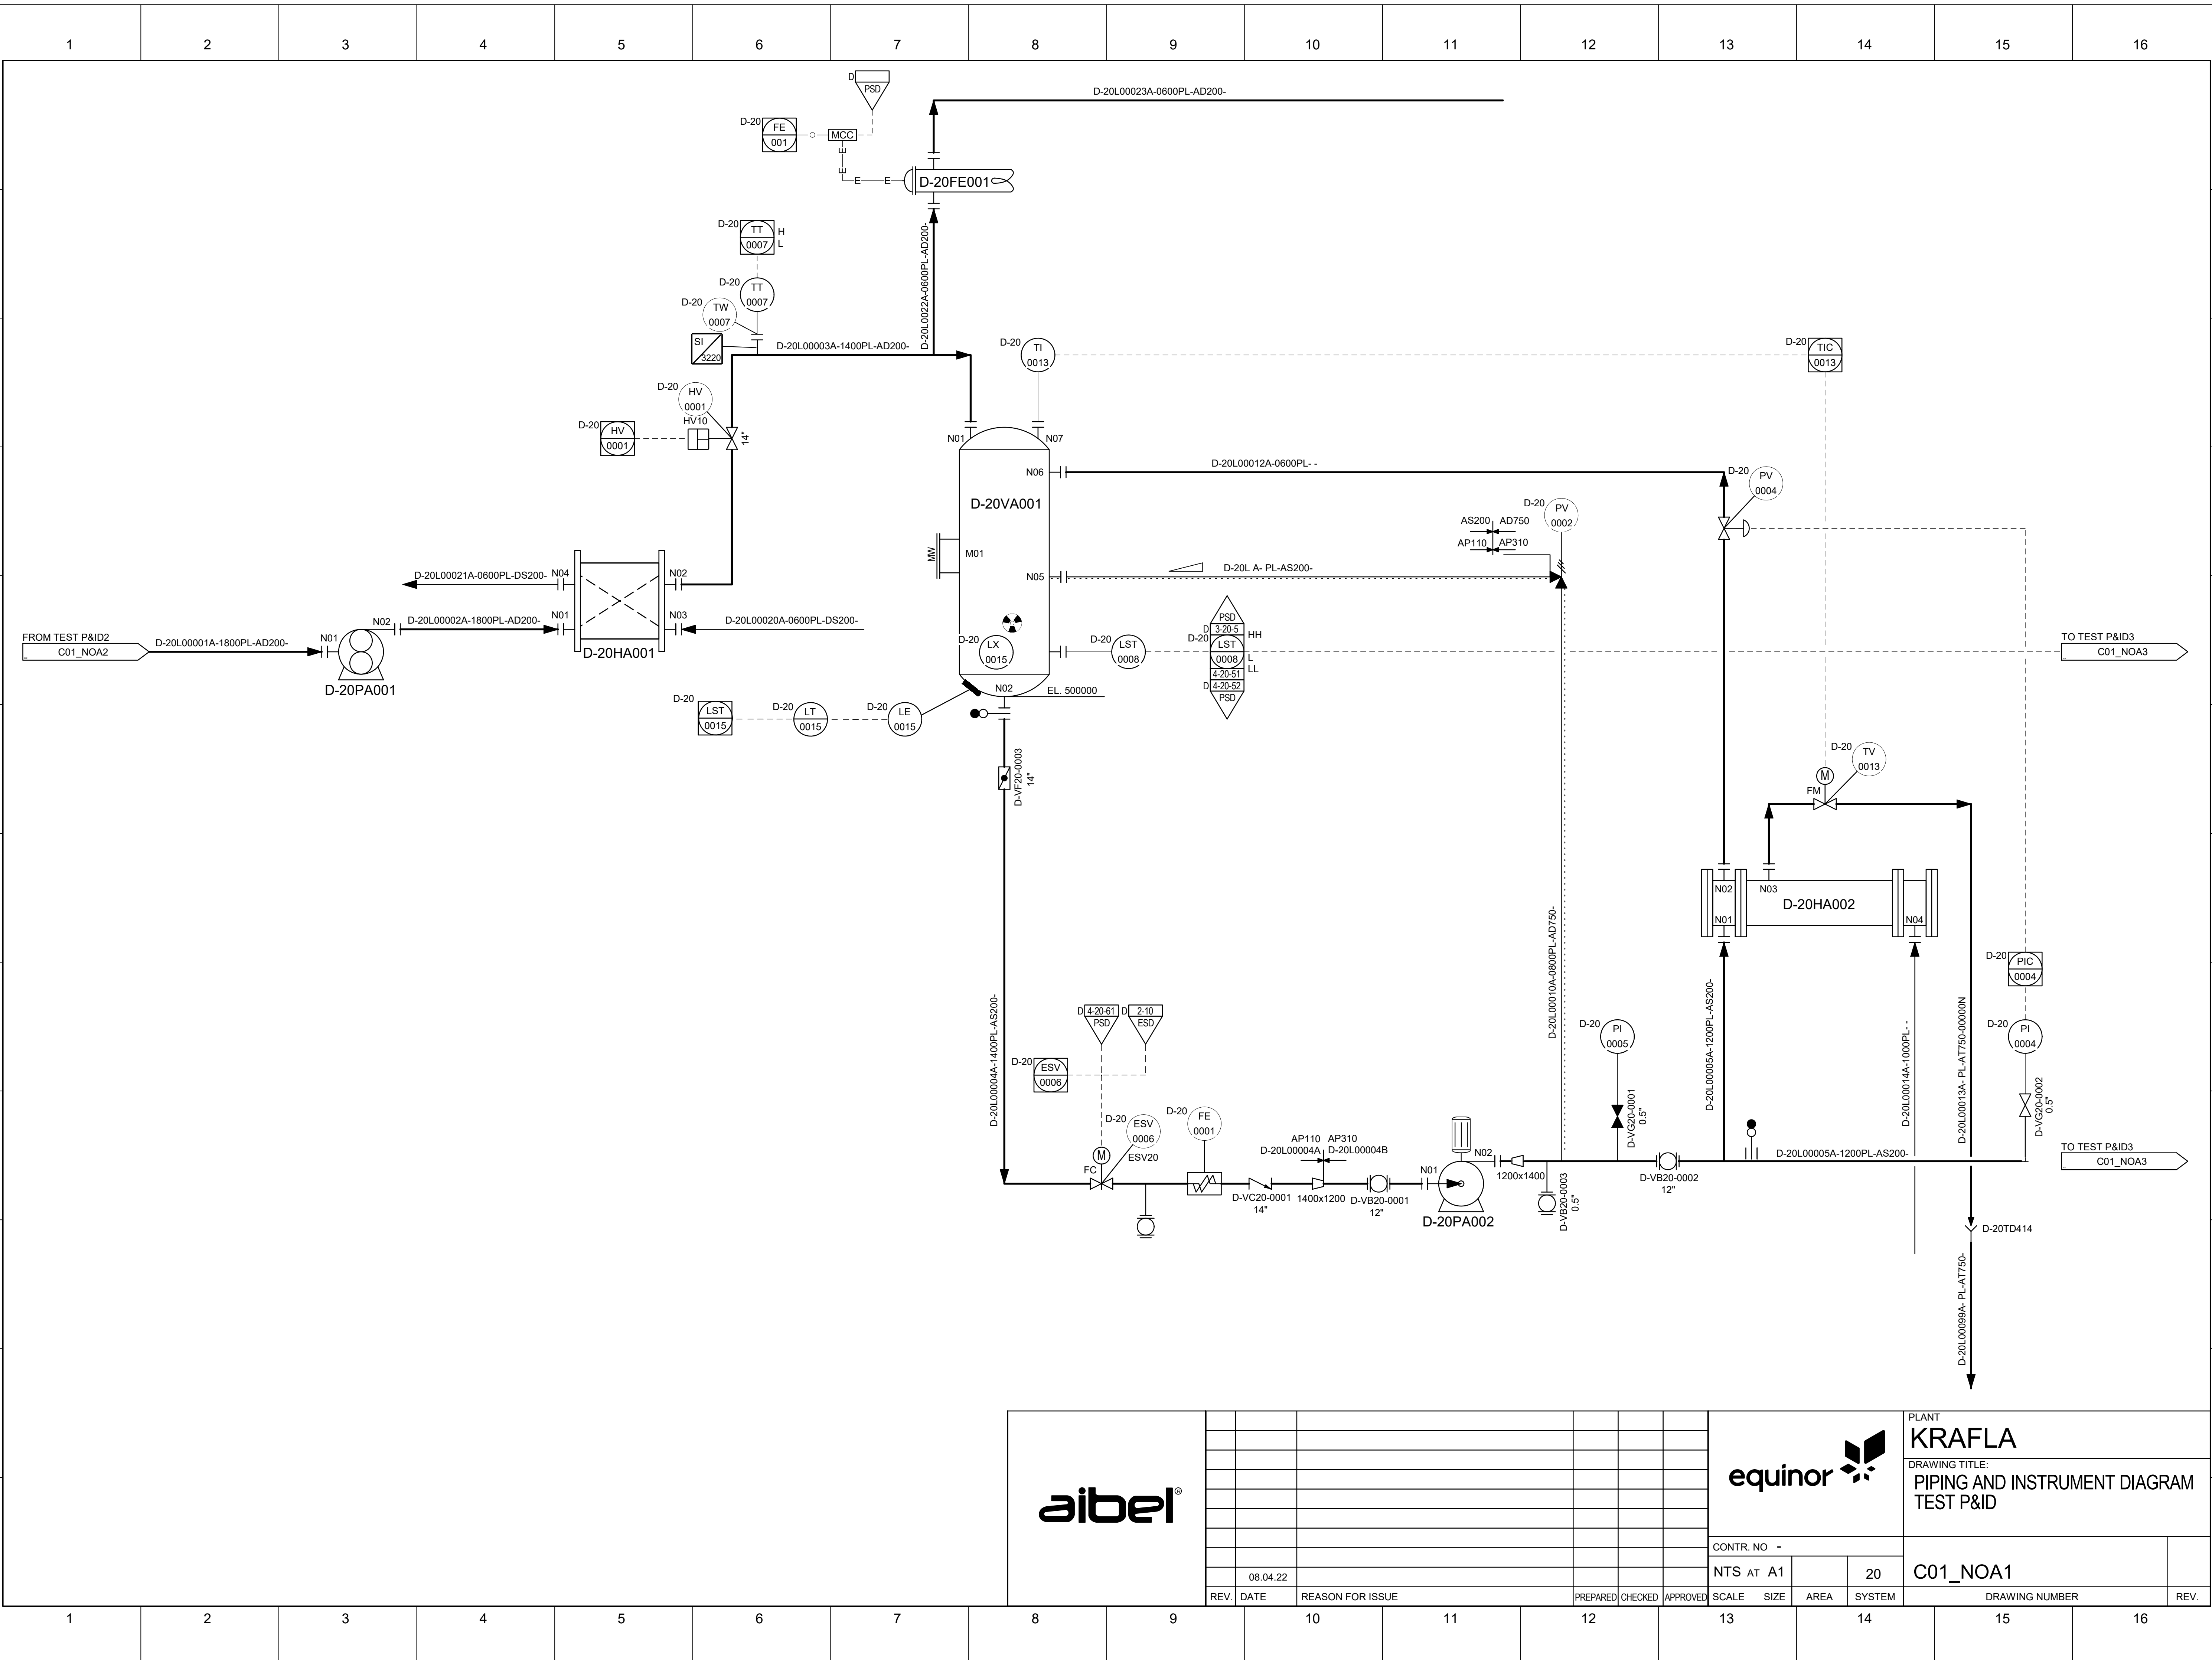

											PLANT KRAFLA			
											DRAWING TITLE: PIPING AND INSTRUMENT DIAGRAM TEST P&ID			
							CONTR. NO -							
		08.04.22						NTS AT A1			20	C01_NOA1		
REV.	DATE	REASON FOR ISSUE			PREPARED	CHECKED	APPROVED	SCALE	SIZE	AREA	SYSTEM	DRAWING NUMBER		REV.