


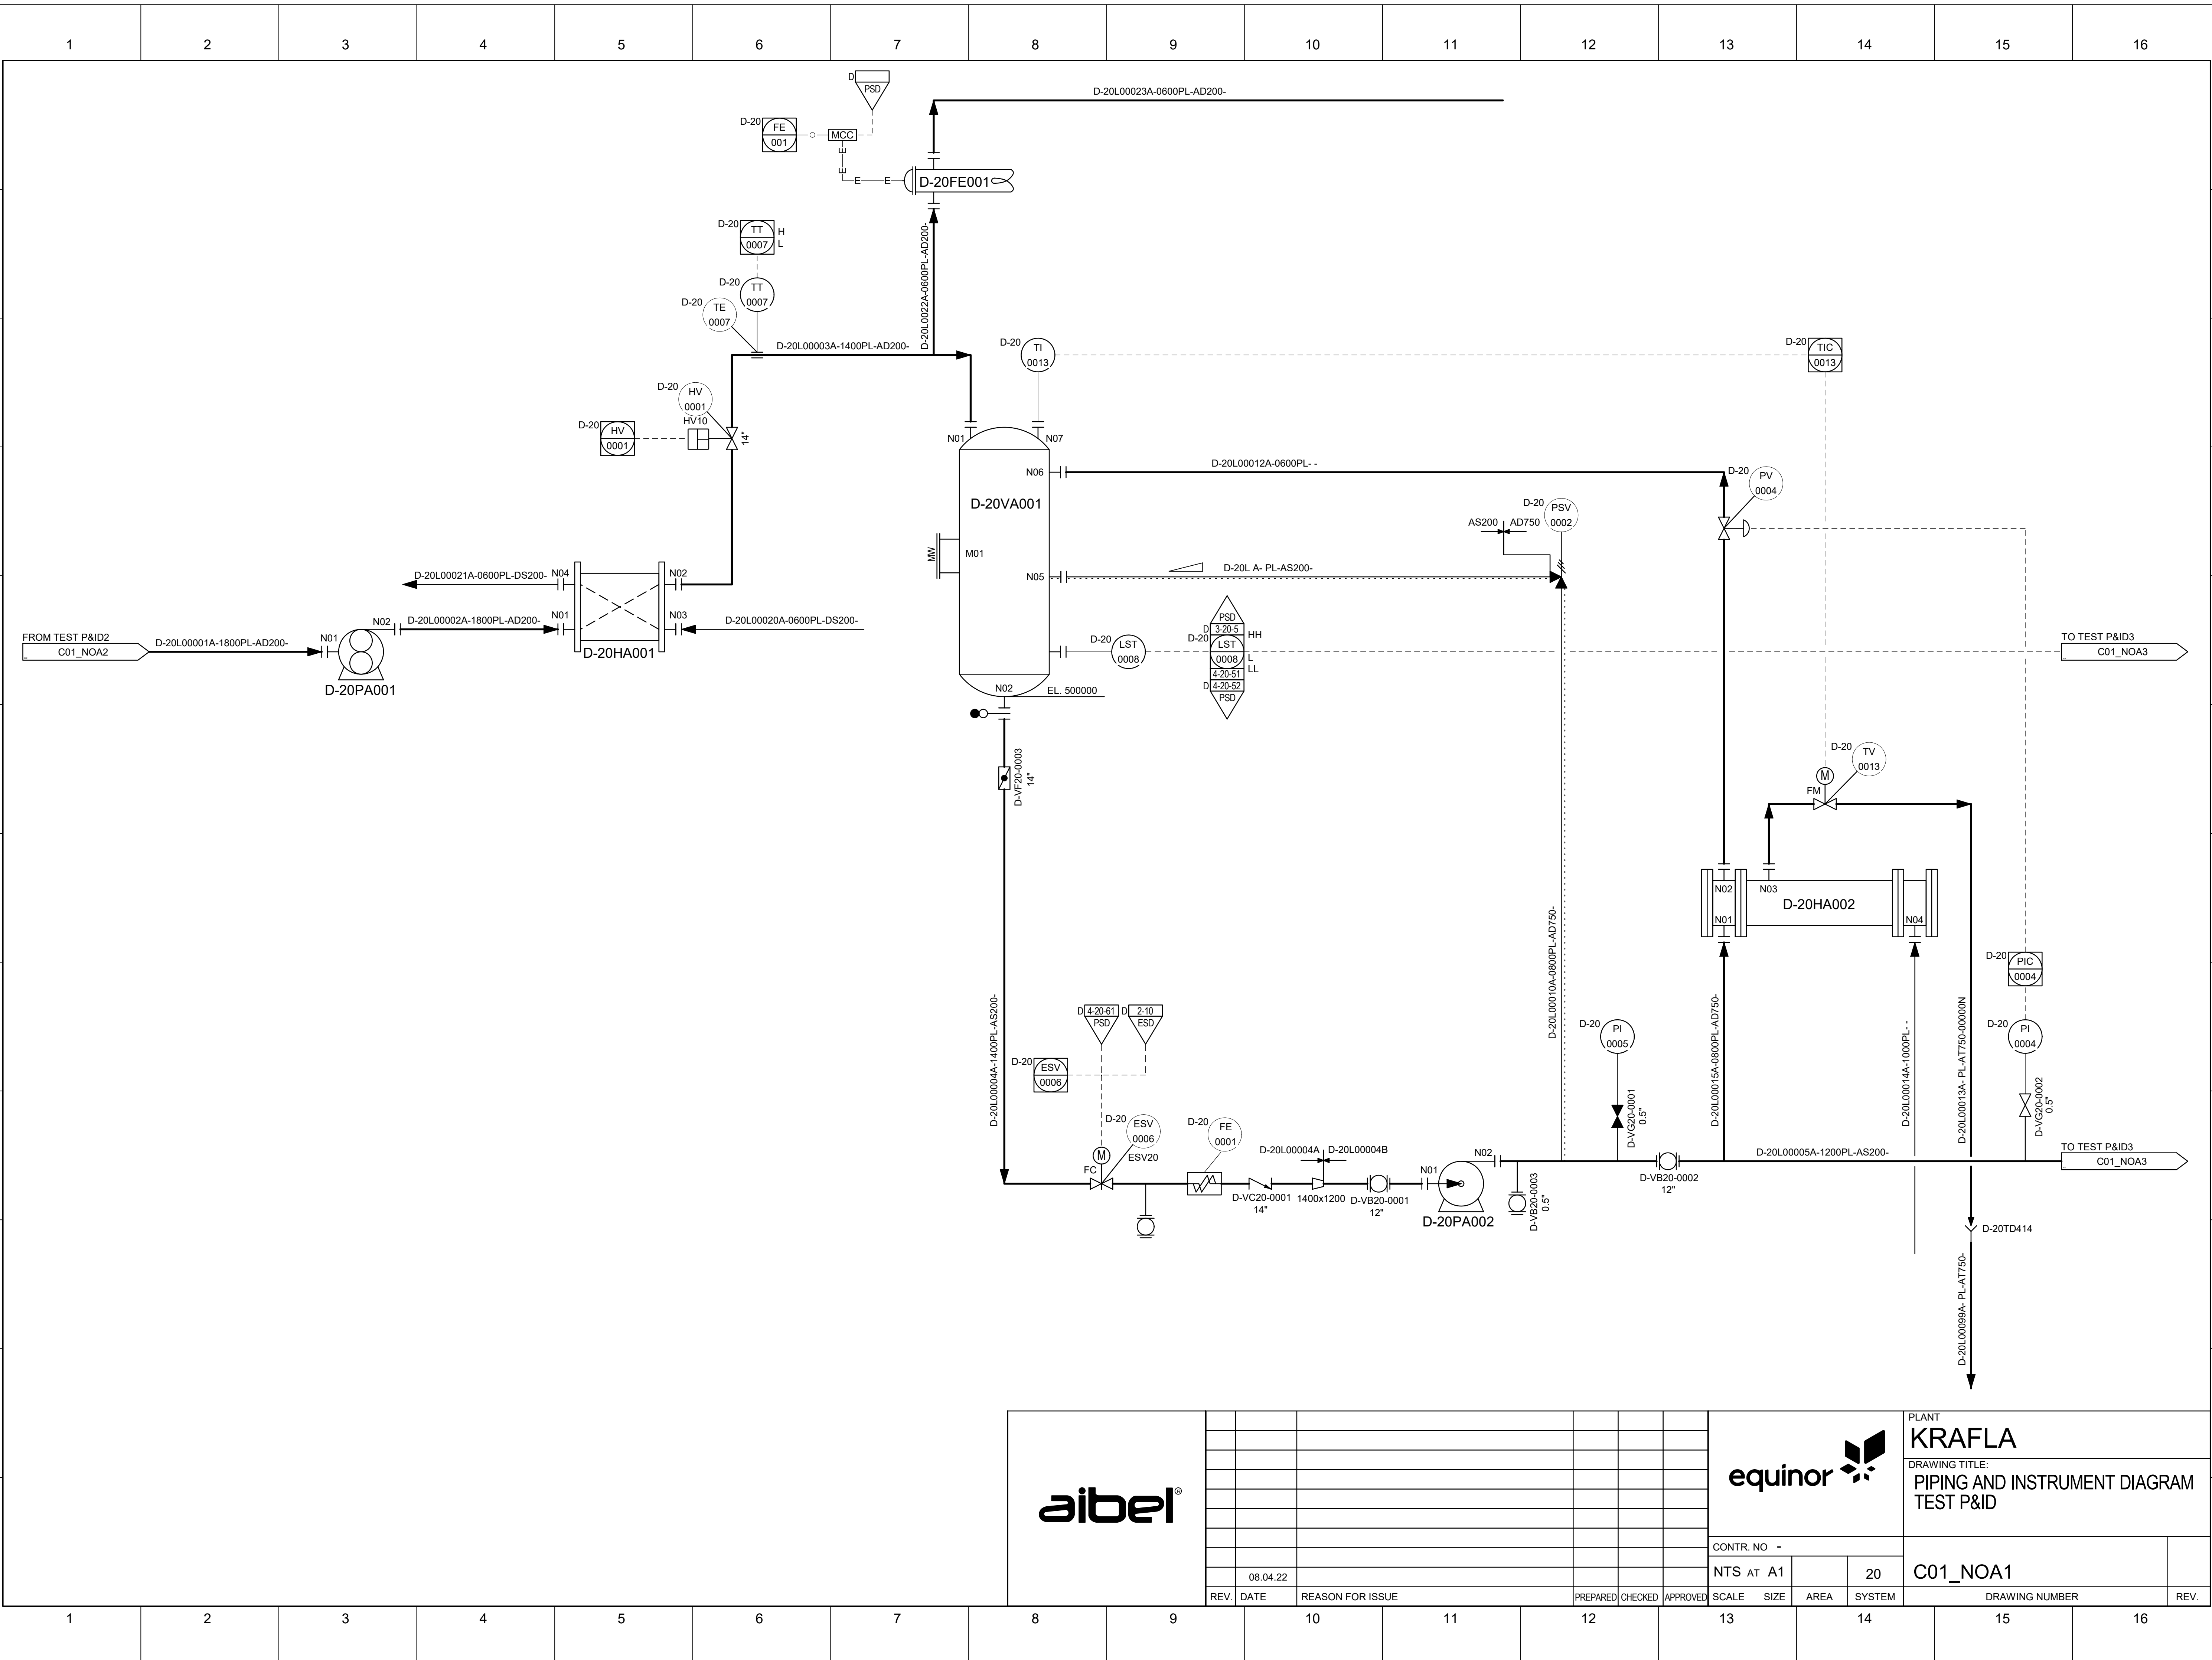

PLANT		KRAFLA	
DRAWING TITLE:		PIPING AND INSTRUMENT DIAGRAM TEST P&ID	
CONTR. NO -			
NTS AT A1		20	C01_NOA1
REV.		DRAWING NUMBER	
REV.			