


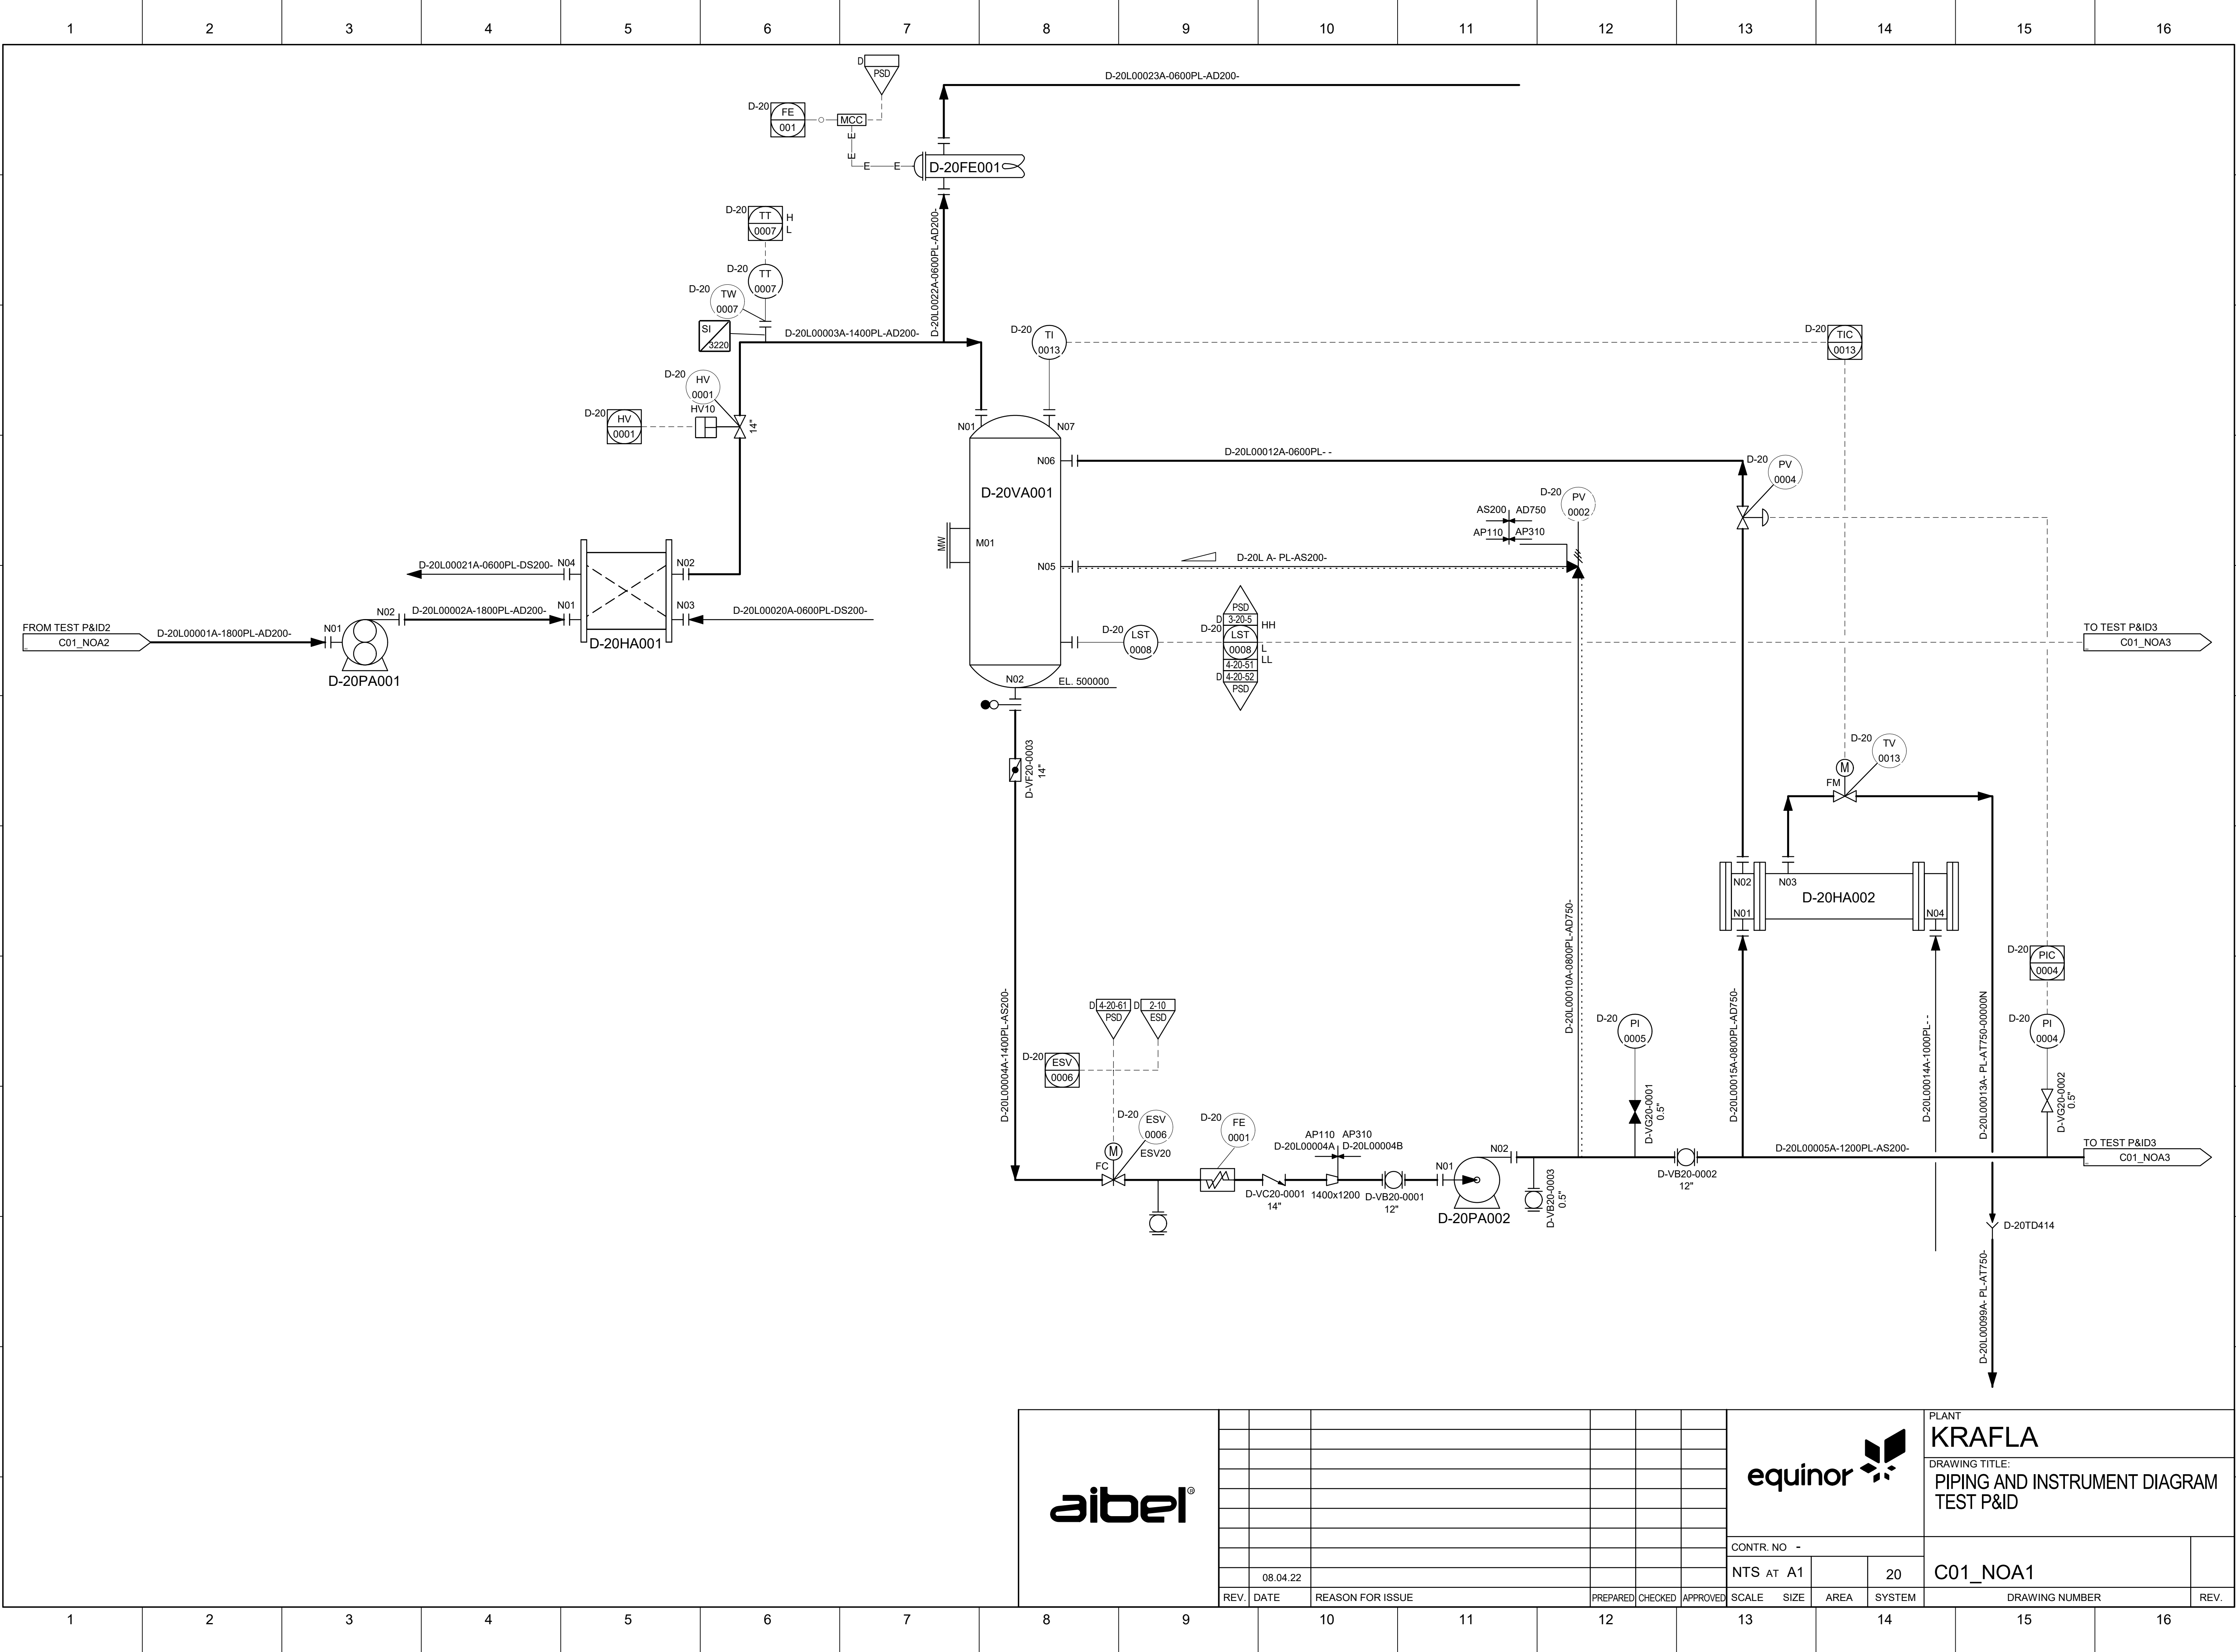

													PLANT KRAFLA		
													DRAWING TITLE: PIPING AND INSTRUMENT DIAGRAM TEST P&ID		
									CONTR. NO -						
									NTS AT A1			20	C01_NOA1		
	REV. DATE				REASON FOR ISSUE				PREPARED		CHECKED	APPROVED	SCALE		REV.