


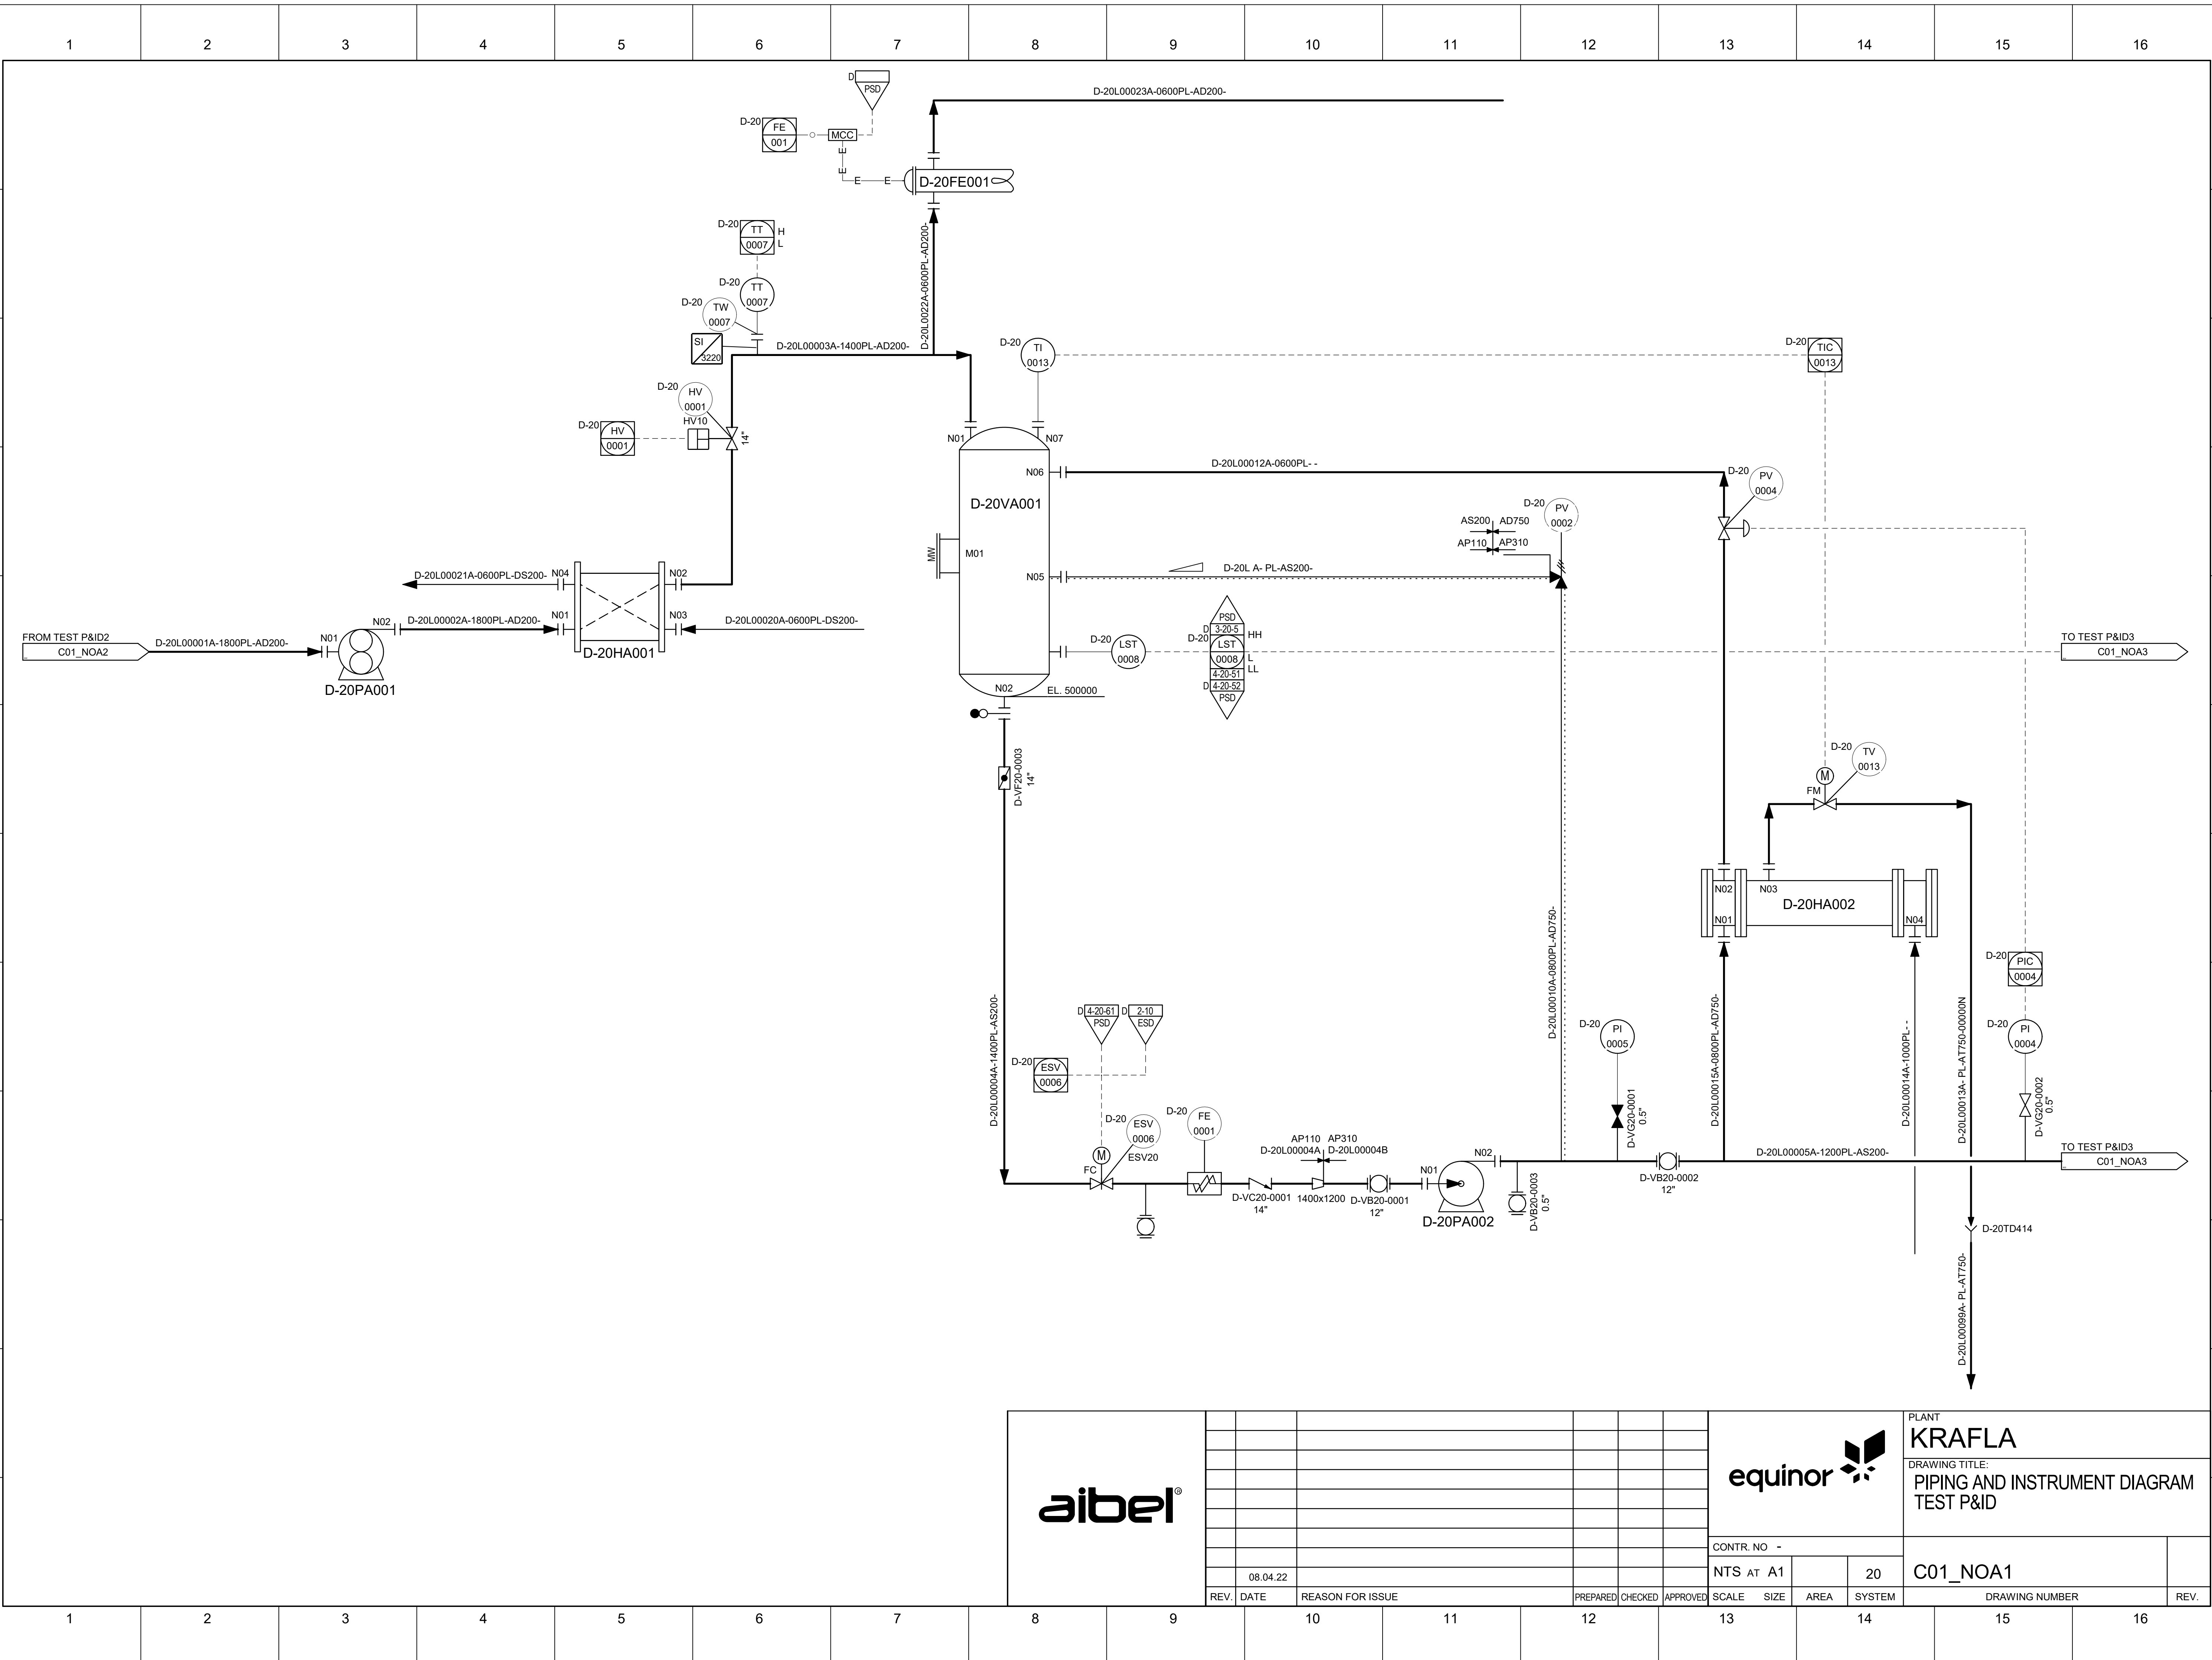

										PLANT		KRAFLA		
										DRAWING TITLE: PIPING AND INSTRUMENT DIAGRAM TEST P&ID				
									CONTR. NO -					
		08.04.22							NTS AT A1		20	C01_NOA1		
REV.	DATE	REASON FOR ISSUE				PREPARED	CHECKED	APPROVED	SCALE	SIZE	AREA	SYSTEM	DRAWING NUMBER	REV.