


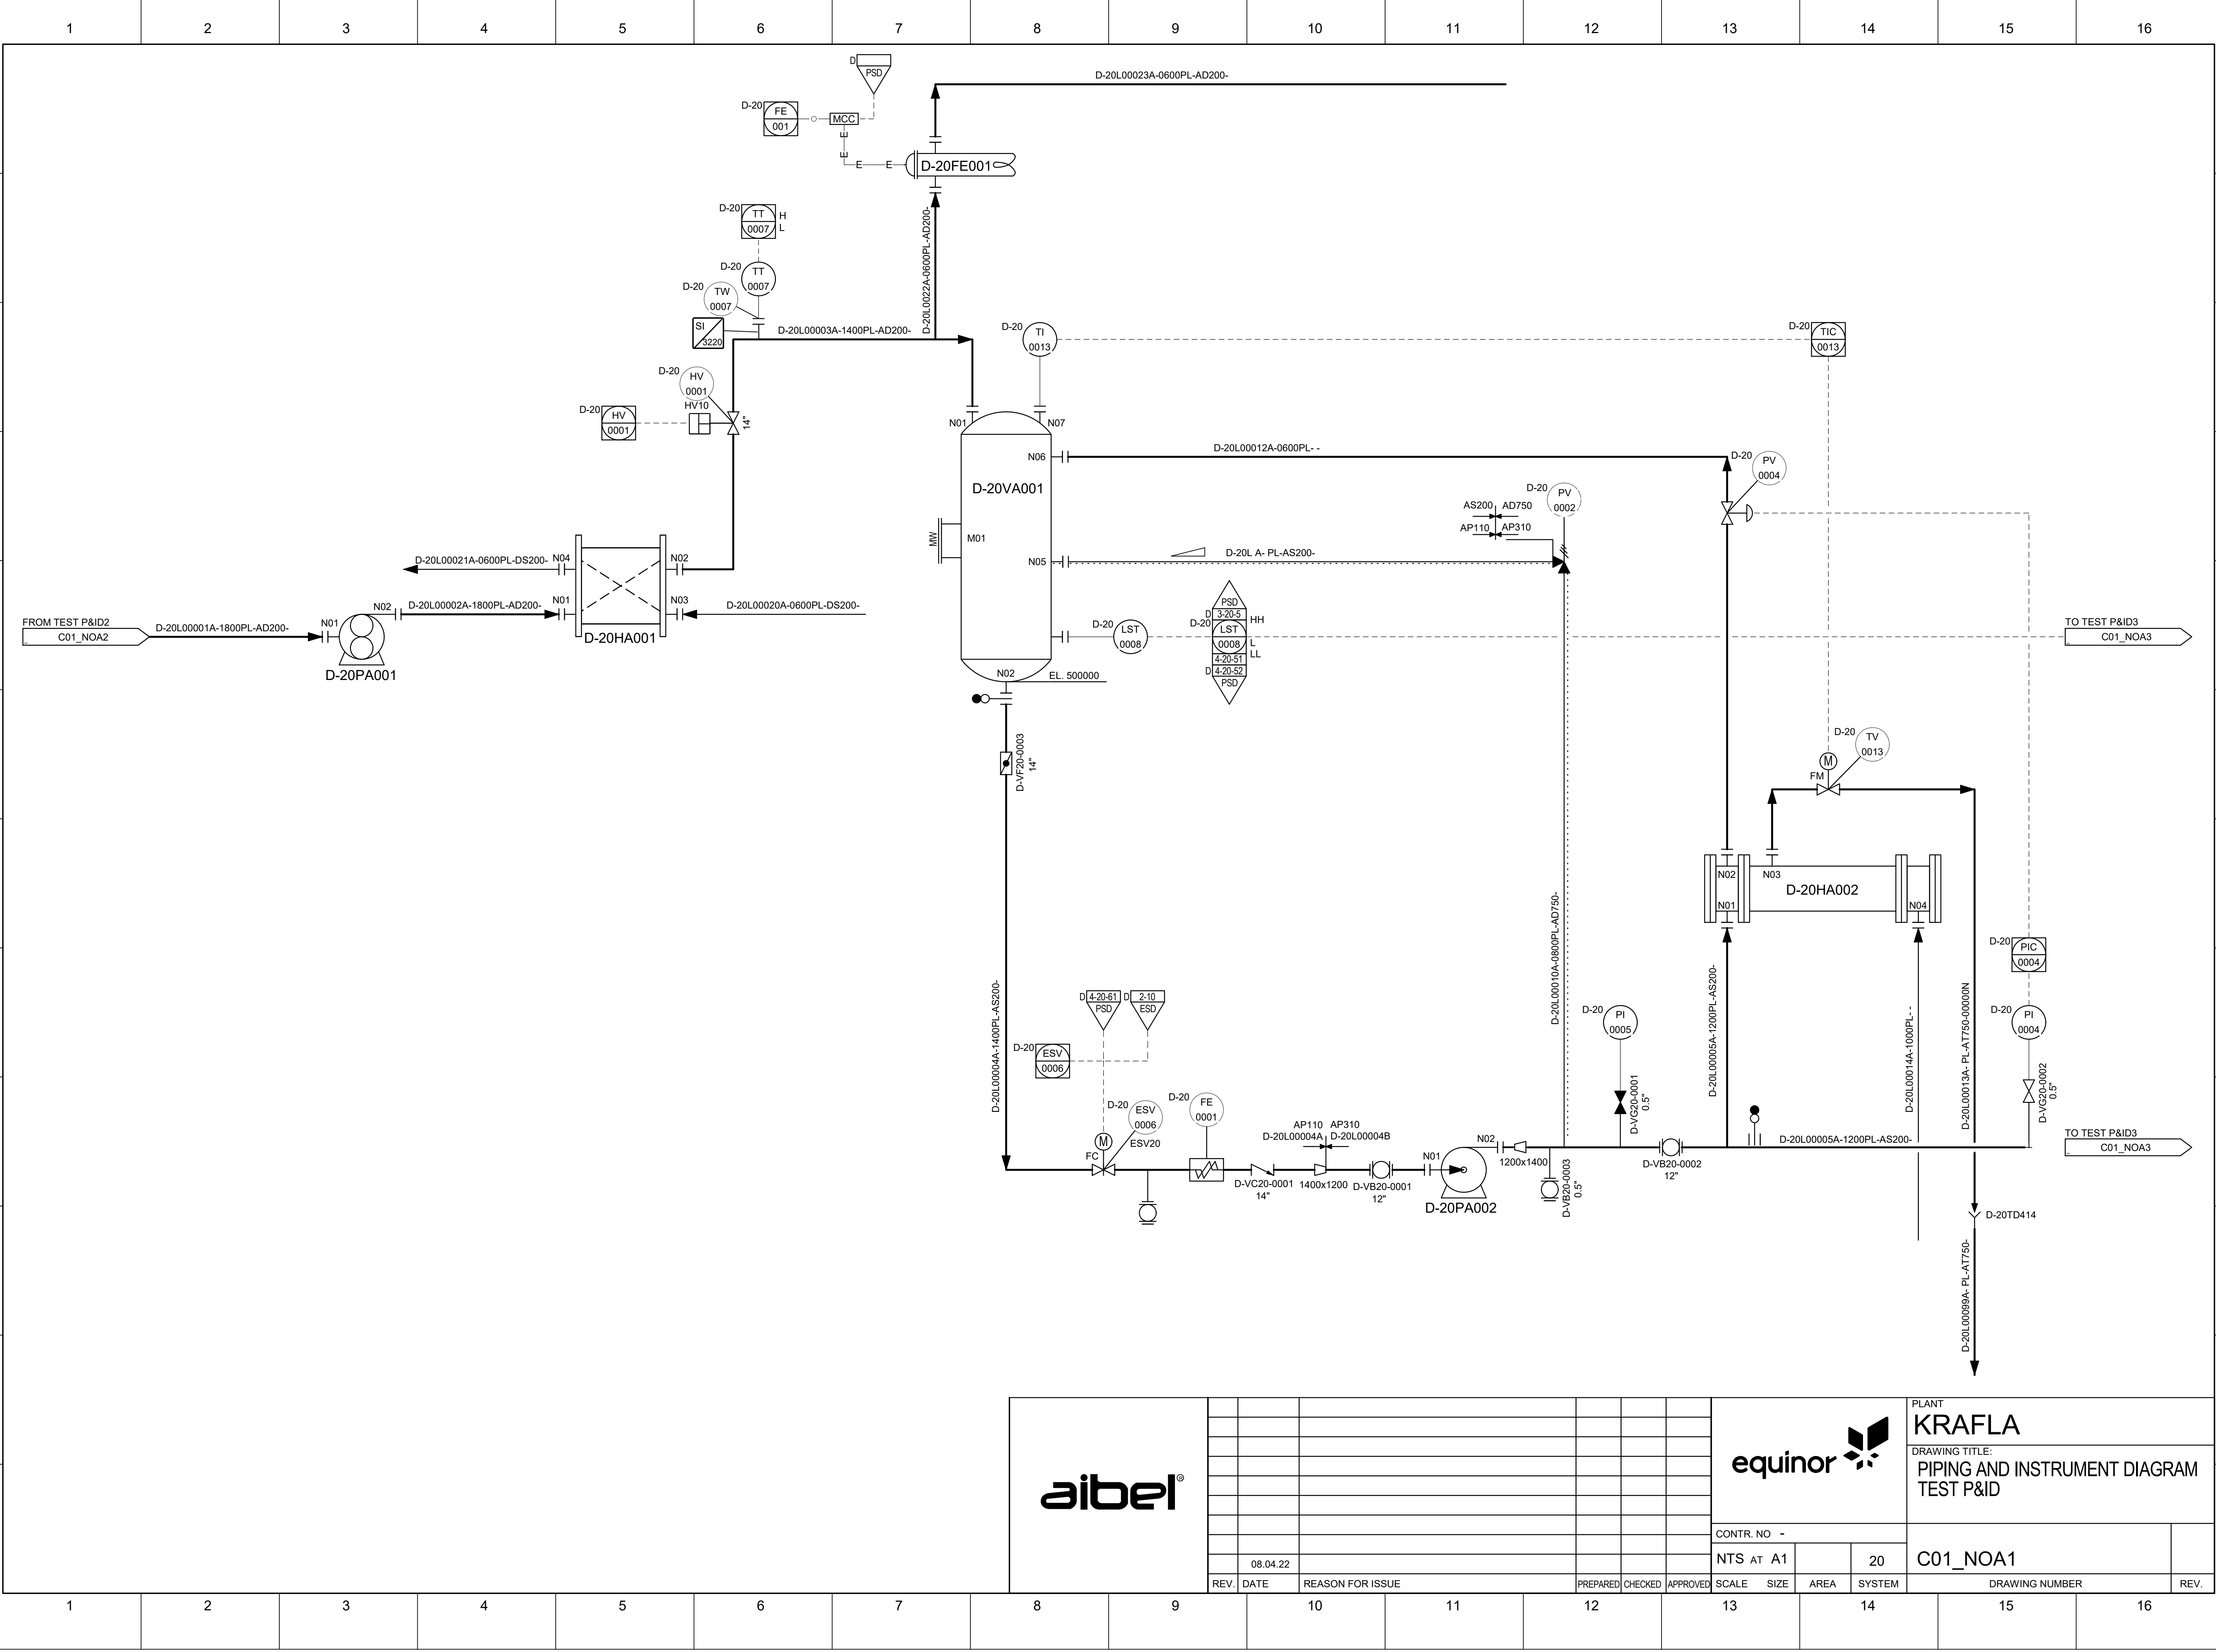

								PLANT		KRAFLA					
								DRAWING TITLE: PIPING AND INSTRUMENT DIAGRAM TEST P&ID							
							CONTR. NO -								
		08.04.22						NTS AT A1			20	C01_NOA1			
REV.	DATE	REASON FOR ISSUE				PREPARED	CHECKED	APPROVED	SCALE	SIZE	AREA	SYSTEM	DRAWING NUMBER		REV.