


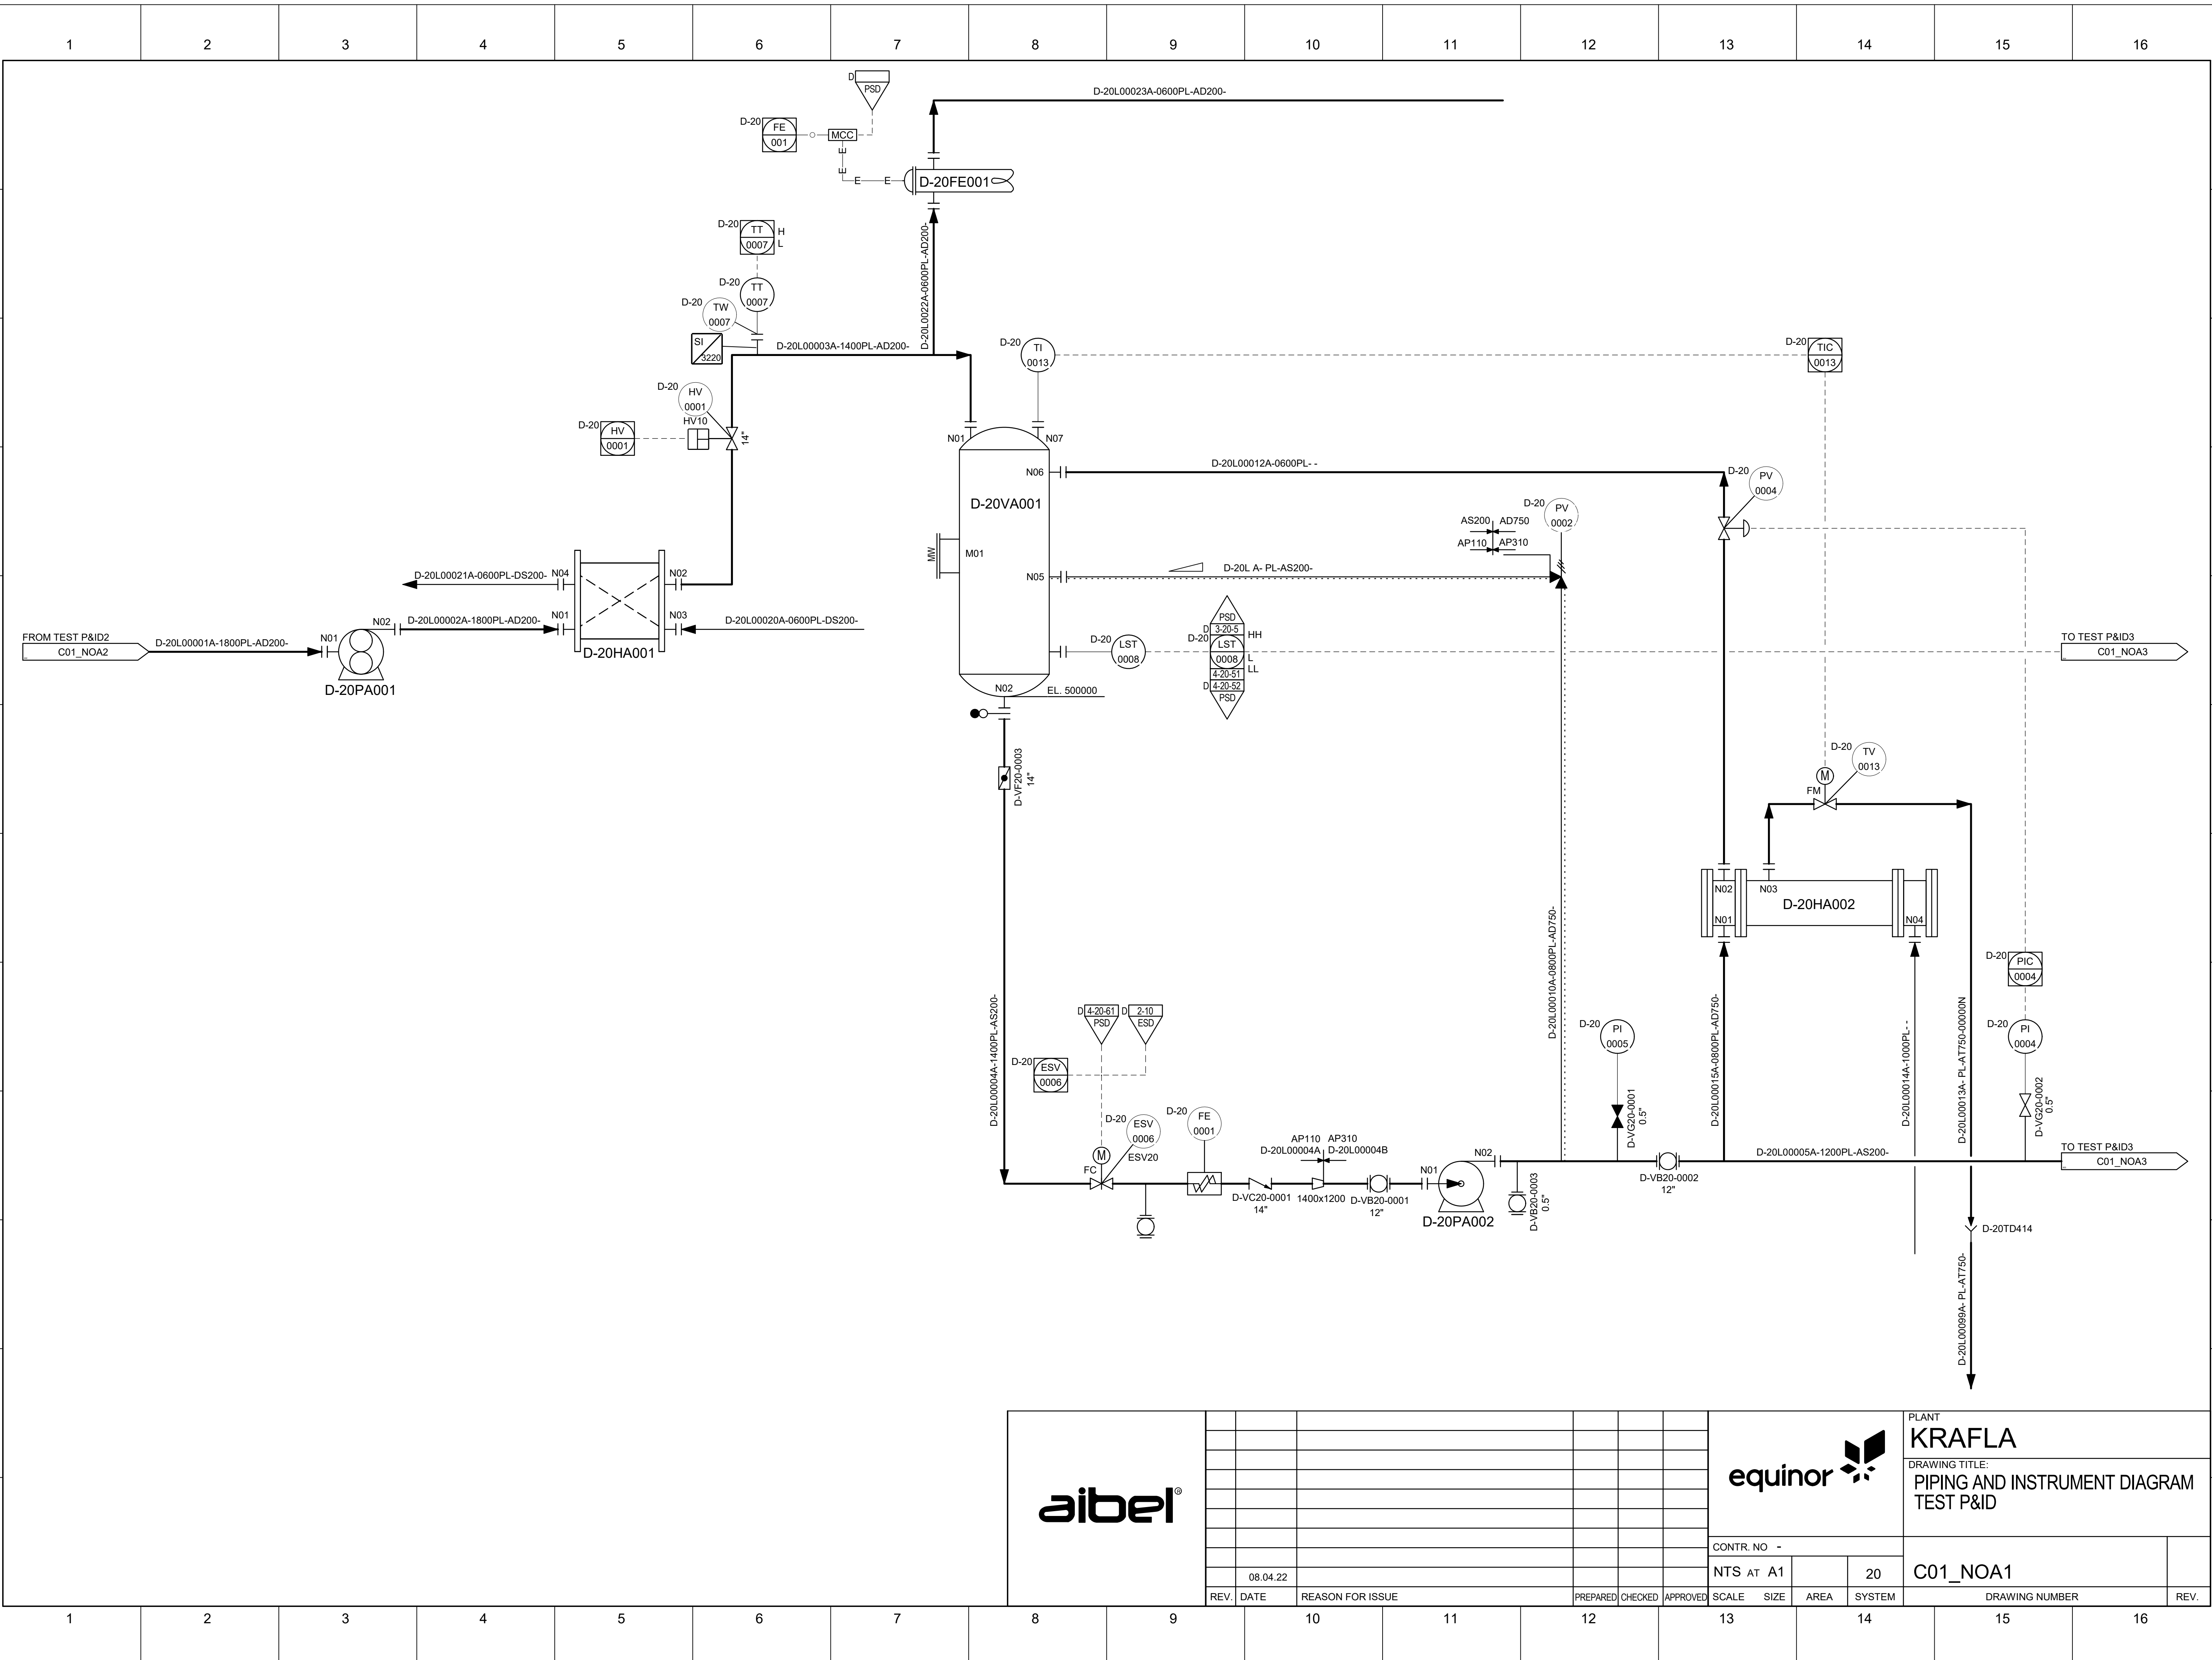

											PLANT		KRAFLA			
											DRAWING TITLE:				PIPING AND INSTRUMENT DIAGRAM	
											TEST P&ID					
											CONTR. NO -					
											NTS AT A1			20	C01_NOA1	
		08.04.22														