


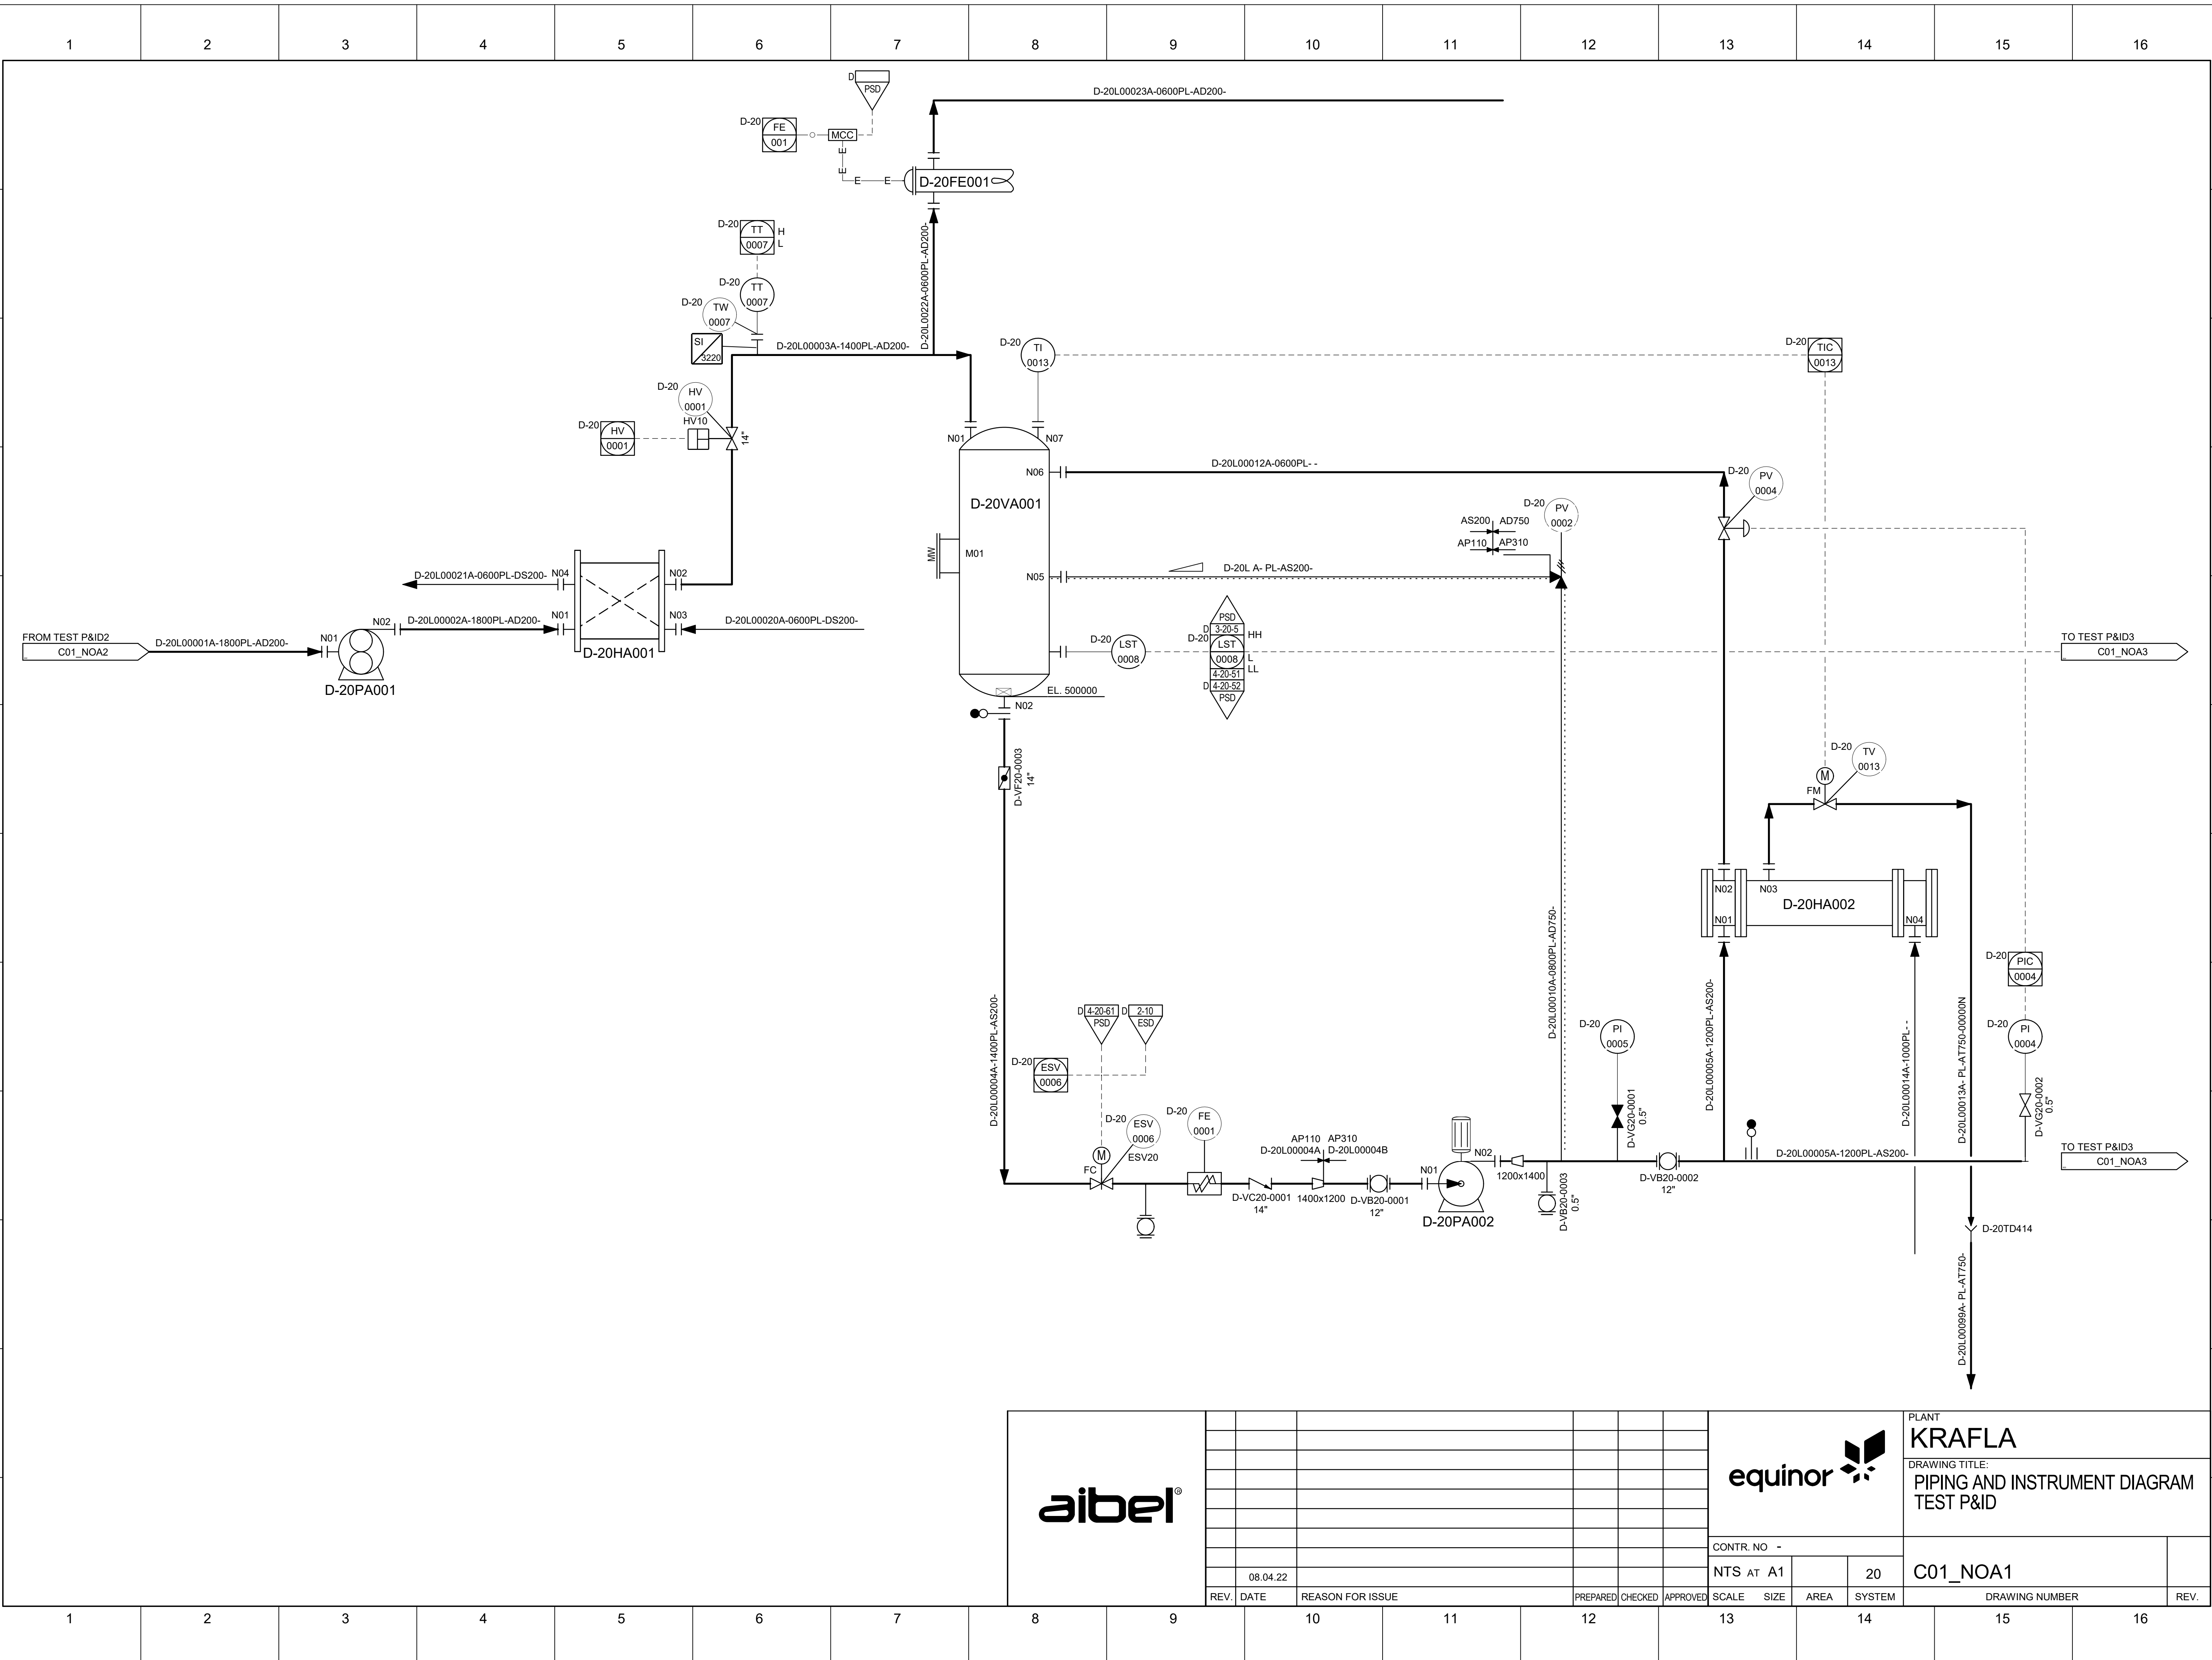

											PLANT		KRAFLA		
											DRAWING TITLE: PIPING AND INSTRUMENT DIAGRAM TEST P&ID				
							CONTR. NO -				C01_NOA1				
		08.04.22					NTS AT A1			20					
	REV.	DATE	REASON FOR ISSUE				PREPARED	CHECKED	APPROVED	SCALE	SIZE	AREA	SYSTEM	DRAWING NUMBER	